




MALHA DE ATERRAMENTO COBERTURA SPDA

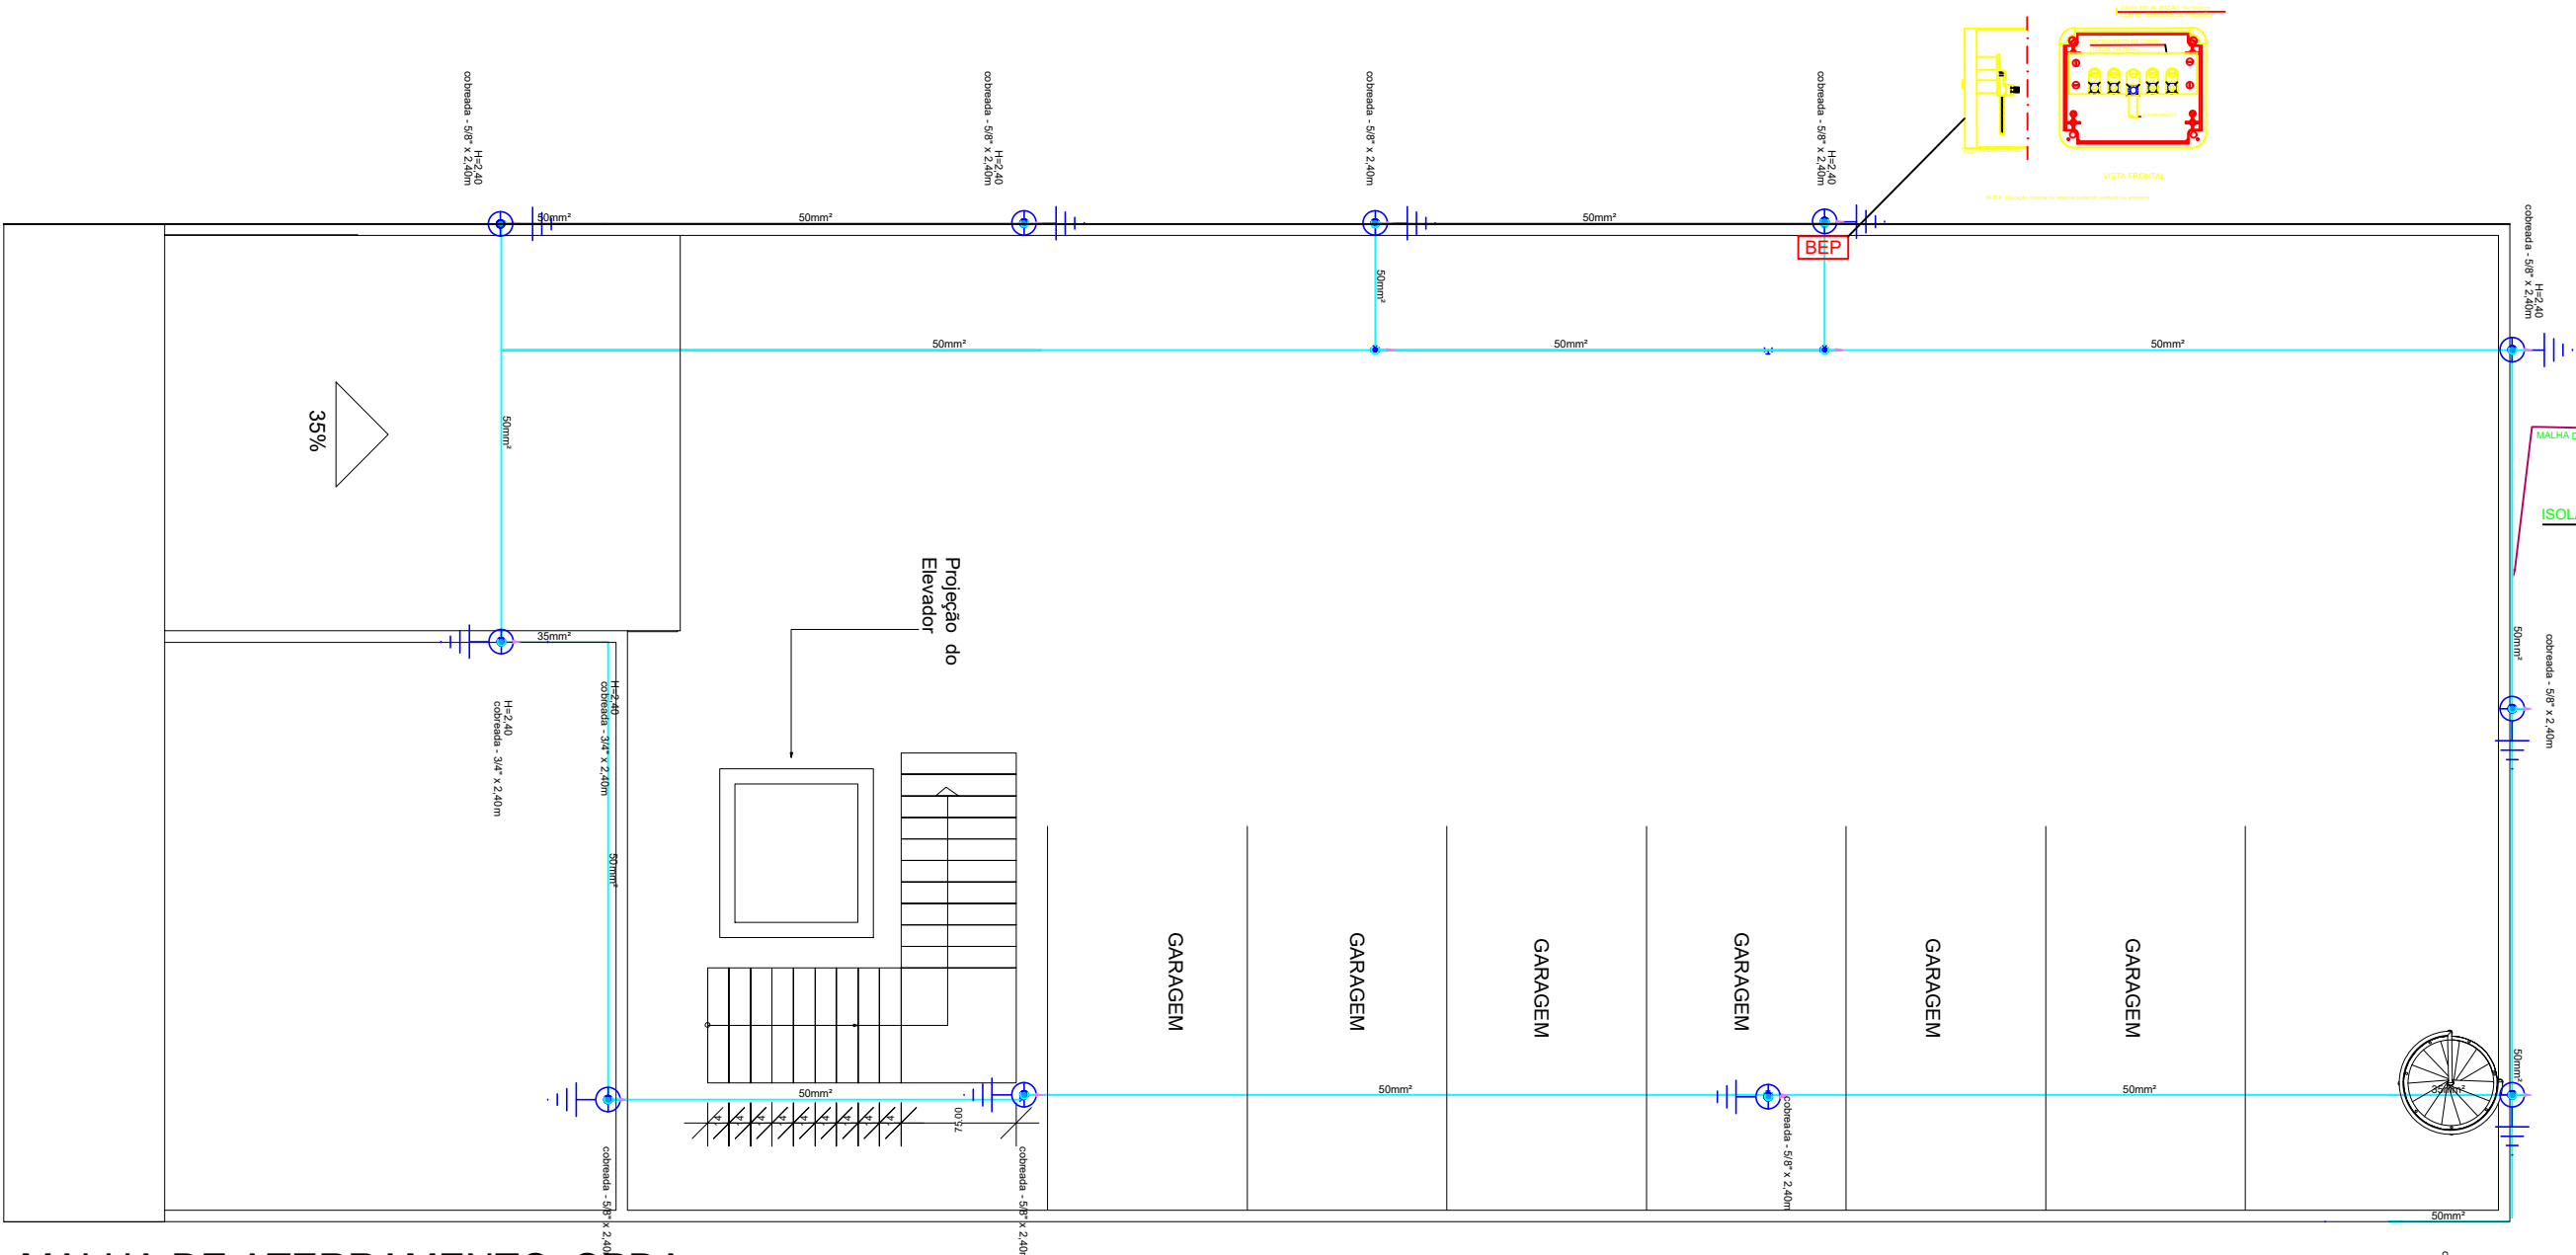


MALHA DE ATERRAMENTO SPDA

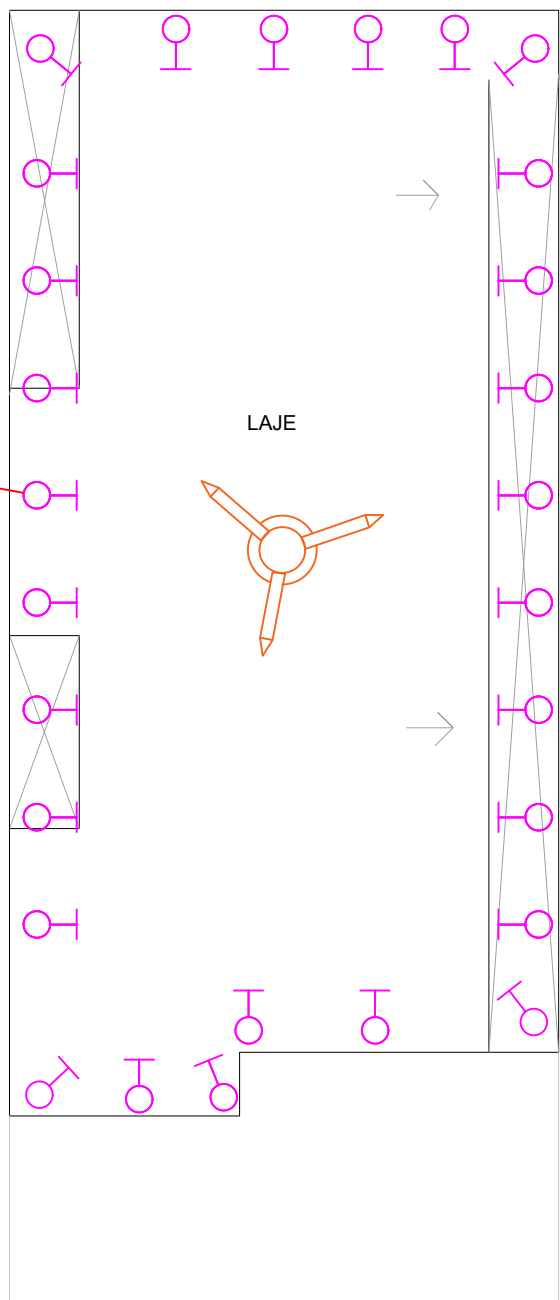


LEGENDA	
	CONEXÃO DE MALHA
	CONEXÃO DE MALHA COM MALHA DE ATERRAMENTO
	CONEXÃO DE MALHA COM MALHA DE ATERRAMENTO
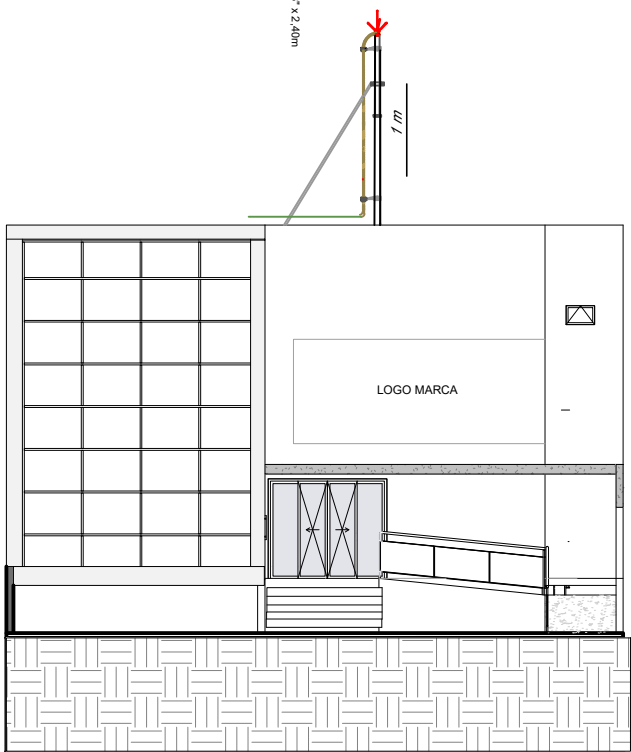


VISTA FACHADA PARA RAIOS

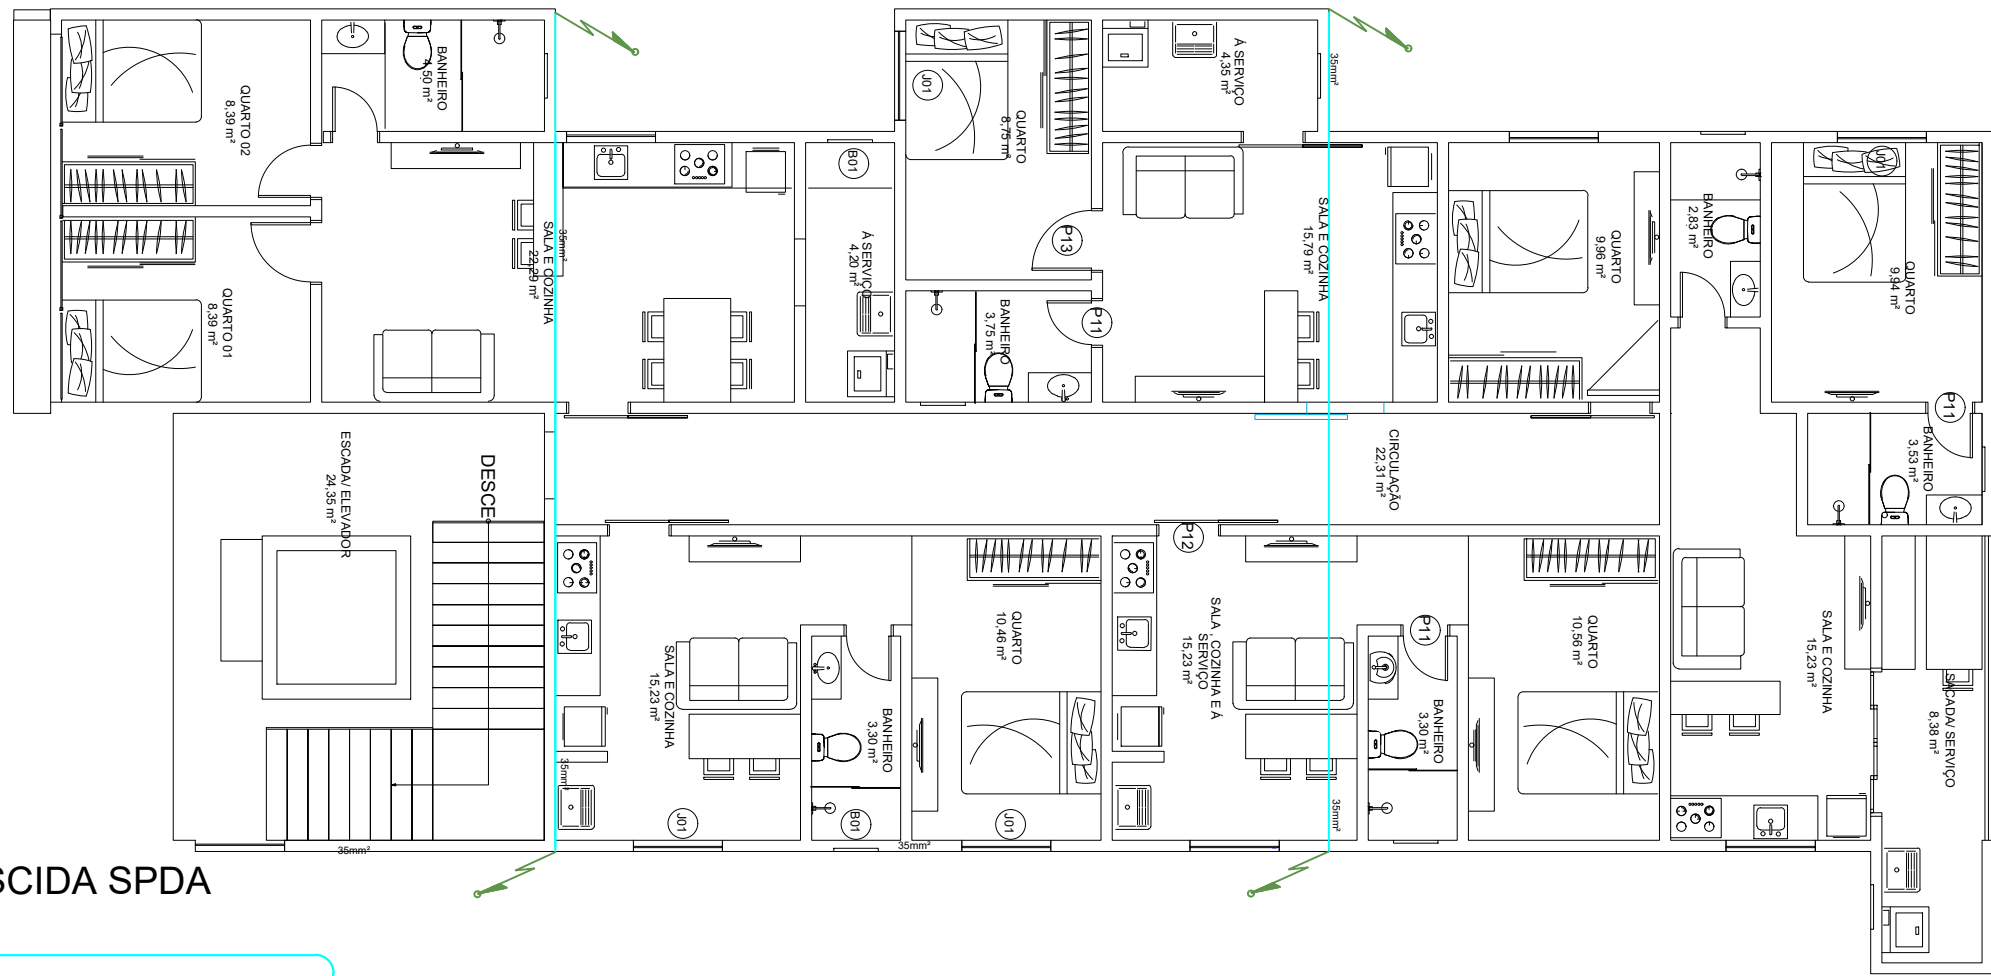


DESCIDA SPDA

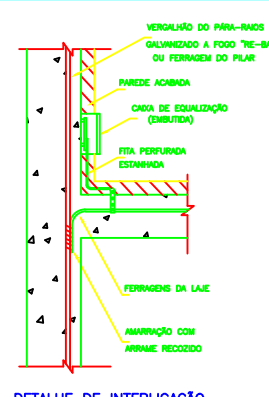

DETALHE DE INTERLIGAÇÃO DA CAIXA DE IGUALIZAÇÃO

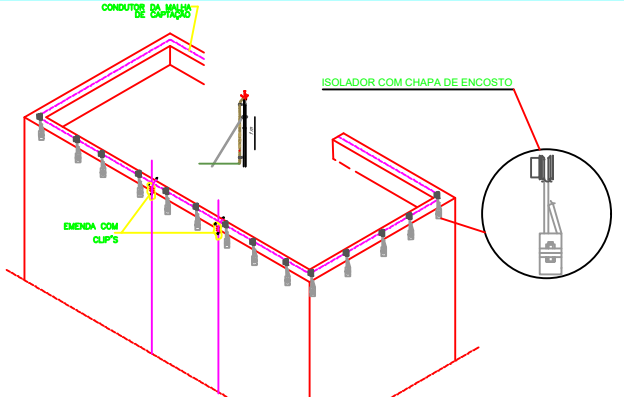


INTERLIGAÇÃO DAS RE-BAR INTERNAS E RE-BAR EXTERNAS

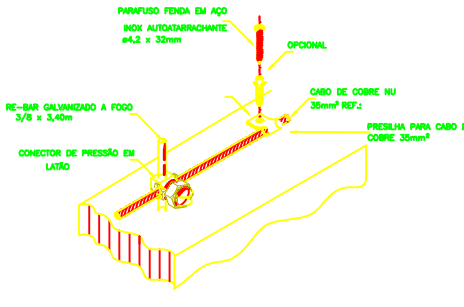


DETALHE DE FIXAÇÃO DO CABO DE COBRE E RE-BAR NA PLATIBANDA


DETALHES DE CAPTAÇÃO E INTERLIGAÇÕES

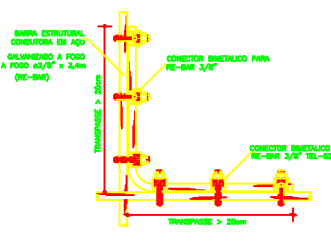


DETALHE DE AMARRAÇÃO DO VERGALHO DE DESCIDA COM O VERGALHO HORIZONTAL

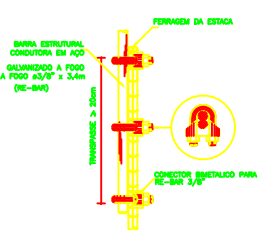

DETALHE DE ENLACE DO VERGALHO DE DESCIDA

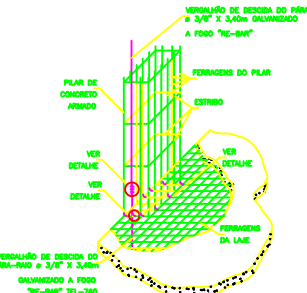


ENCONTRO DAS FERRAGENS DAS LAJES COM AS FERRAGENS DOS PLATIBANDAS

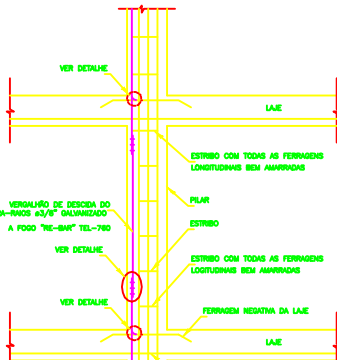


PE DIRETO GENÉRIO E AMARRAÇÕES


DETALHES DE DESCIDAS E INTERLIGAÇÕES

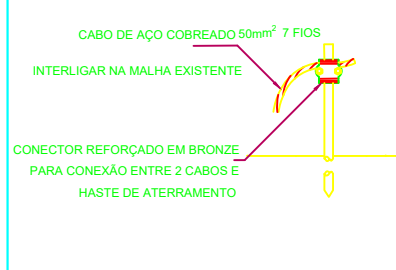


DETALHE DE AMARRAÇÃO DO VERGALHO DE DESCIDA COM O VERGALHO HORIZONTAL

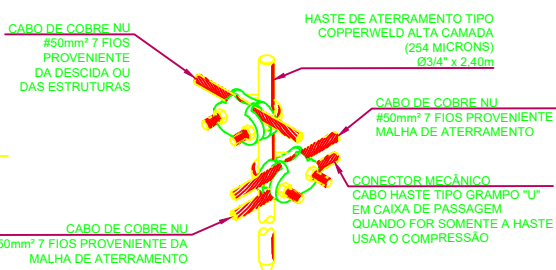


DETALHE DE ENLACE DO VERGALHO DE DESCIDA

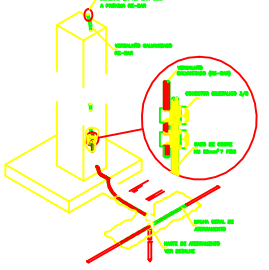


ENCONTRO DAS FERRAGENS DAS LAJES COM AS FERRAGENS DOS PLATIBANDAS

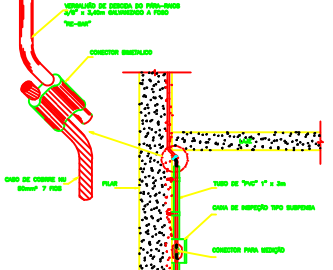

DETALHE DE AMARRAÇÃO DO VERGALHO DE DESCIDA COM O VERGALHO HORIZONTAL

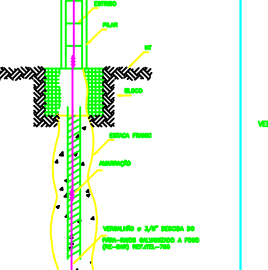


DETALHE DE ENLACE DO VERGALHO DE DESCIDA

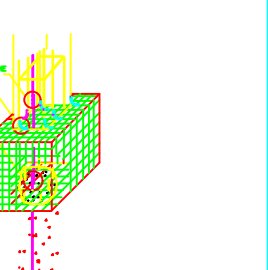


ENCONTRO DAS FERRAGENS DAS LAJES COM AS FERRAGENS DOS PLATIBANDAS


DETALHES DE ATERRAMENTO E INTERLIGAÇÕES

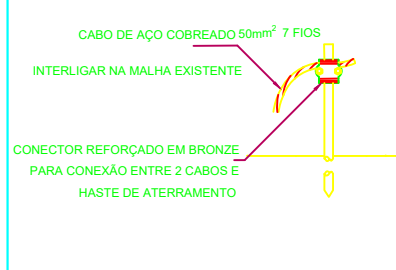


DETALHE DE AMARRAÇÃO DO VERGALHO DE DESCIDA COM O VERGALHO HORIZONTAL

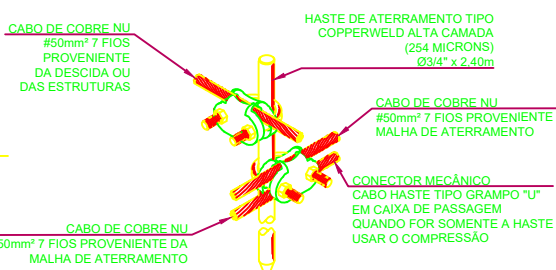


DETALHE DE ENLACE DO VERGALHO DE DESCIDA

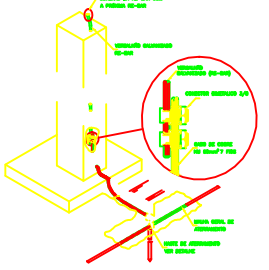


ENCONTRO DAS FERRAGENS DAS LAJES COM AS FERRAGENS DOS PLATIBANDAS

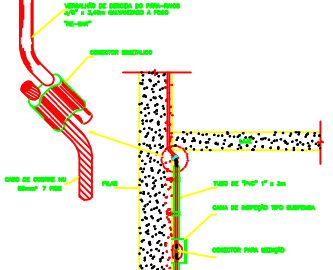

DETALHE DE AMARRAÇÃO DO VERGALHO DE DESCIDA COM O VERGALHO HORIZONTAL

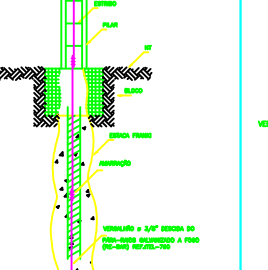

DETALHE DE ENLACE DO VERGALHO DE DESCIDA

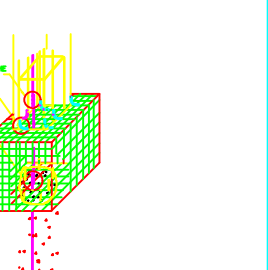

ENCONTRO DAS FERRAGENS DAS LAJES COM AS FERRAGENS DOS PLATIBANDAS