

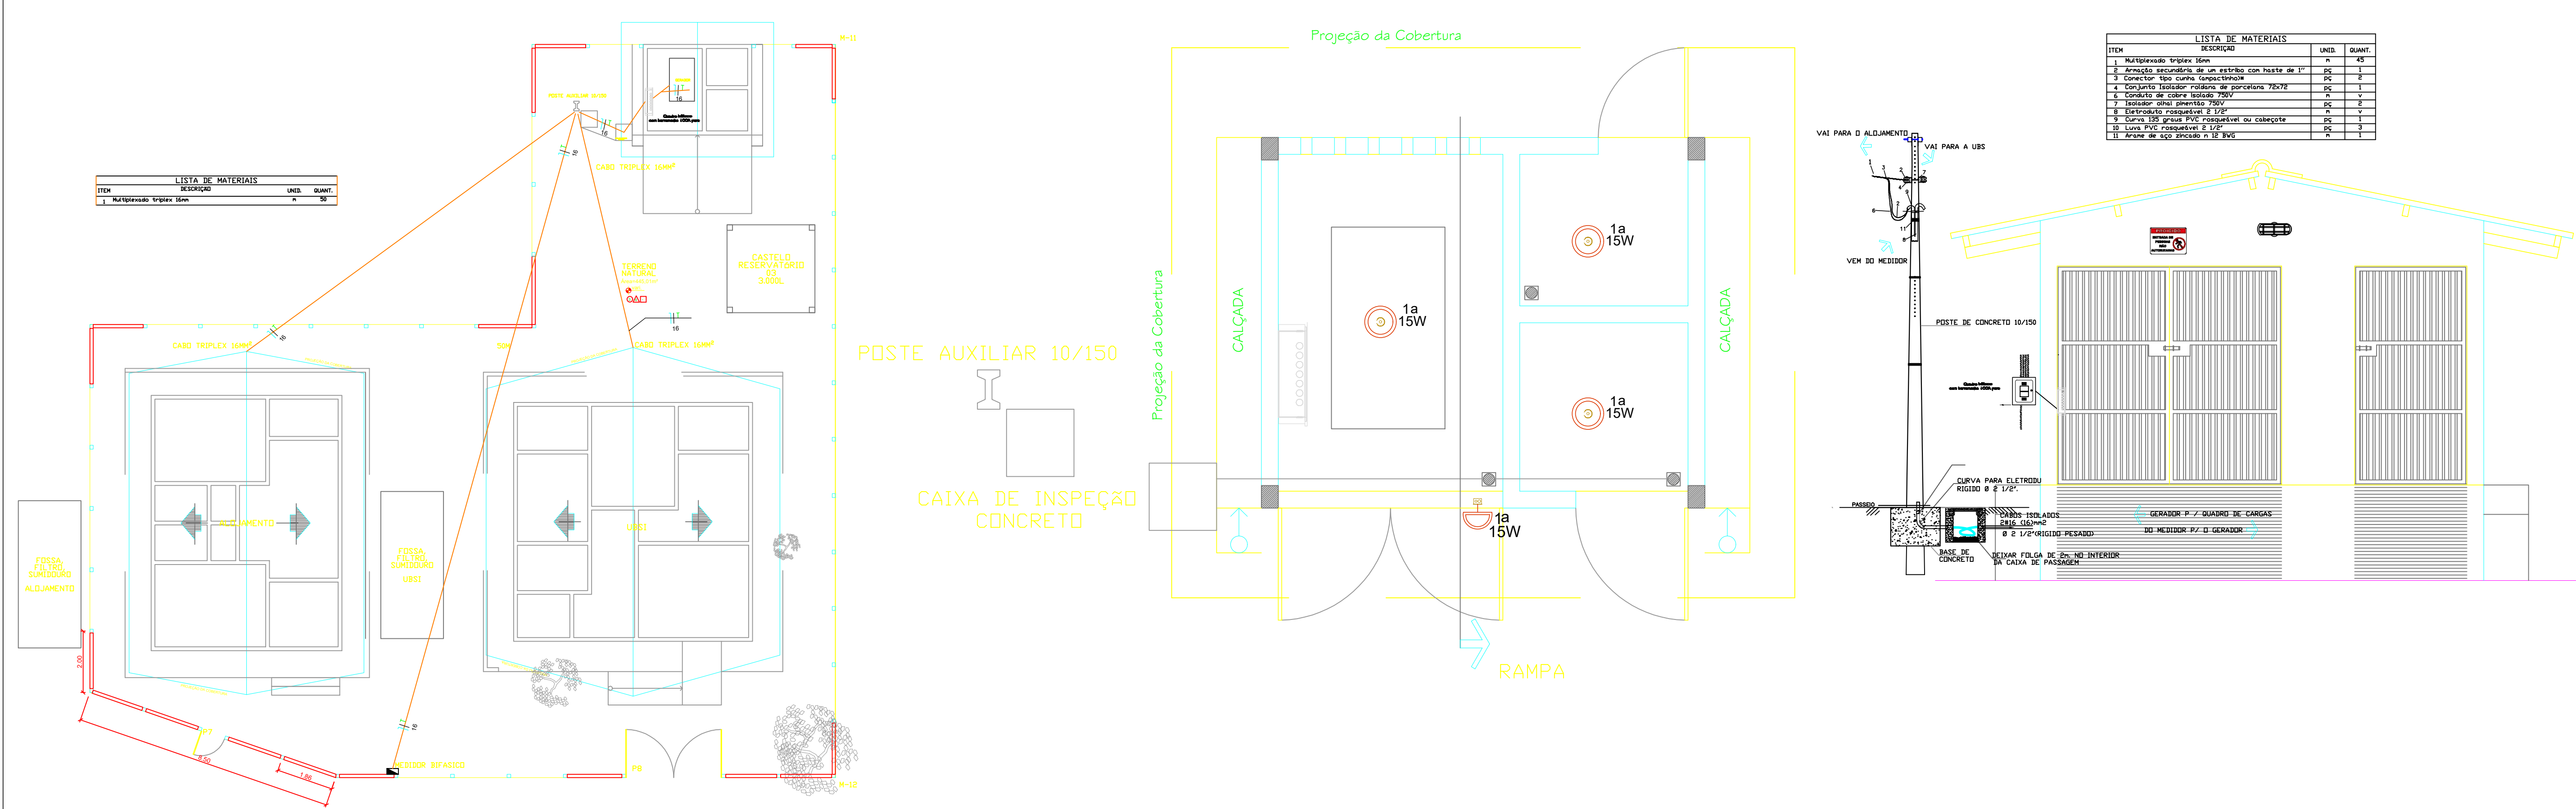


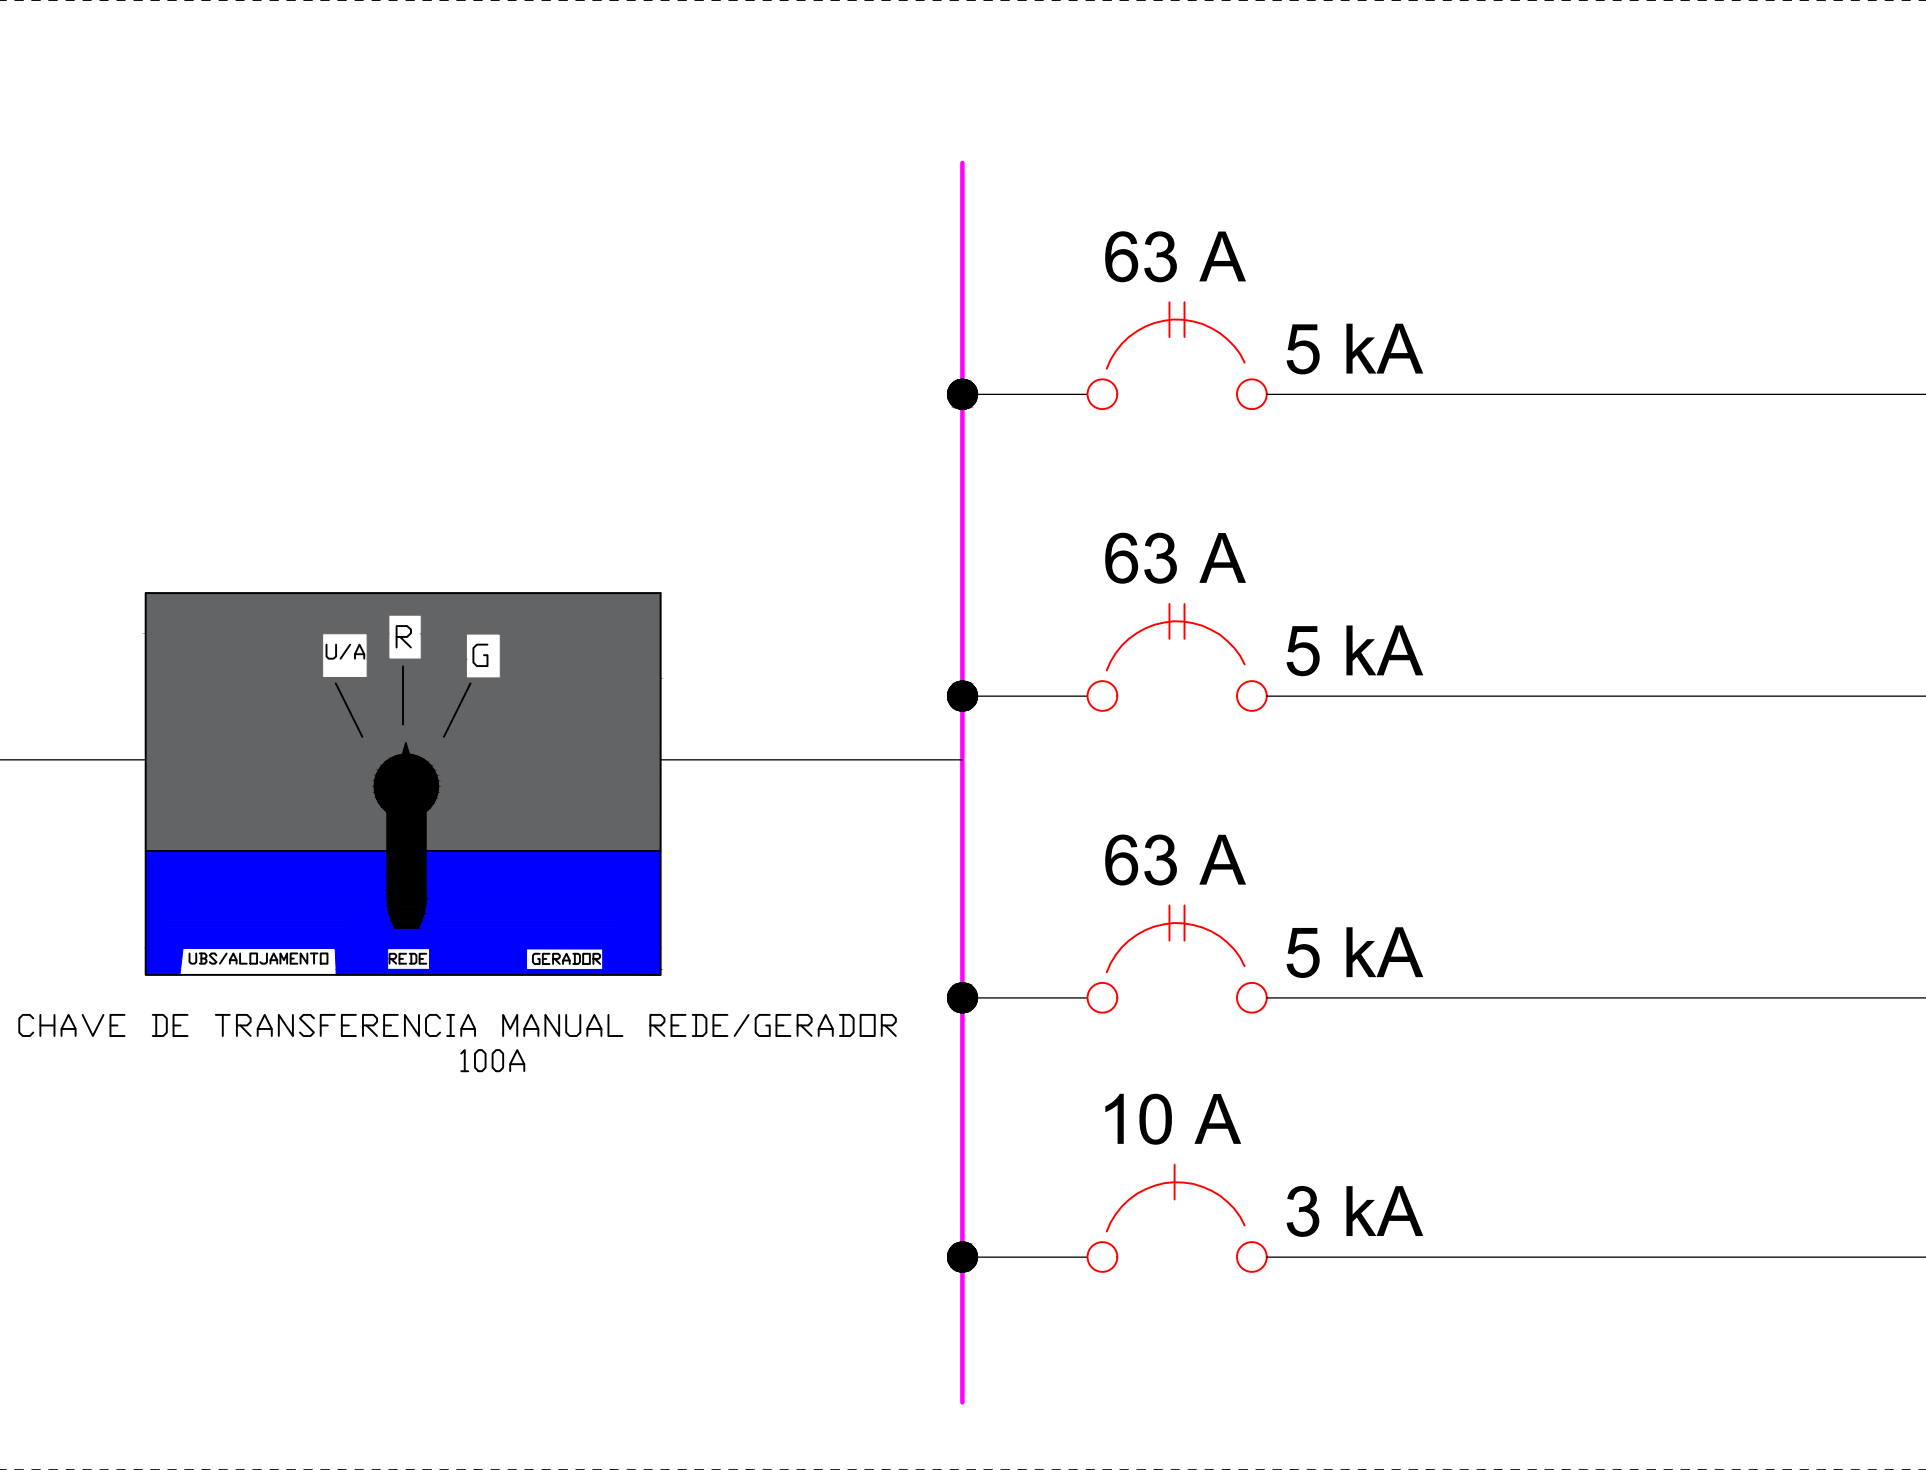

LISTA DE MATERIAIS		
ITEM	DESCRIÇÃO	QUANT.
1	Multiplexado triplex 16mm	n
2	Armação secundária de um estribo com haste de 1"	PC
3	Conector tipo curva Impactation	PC
4	Conjunto Isolador rolante de porcelana 75kV	PC
5	Conduto de cobre isolado 75kV	n
6	Isolador ômega pinheiro 75kV	PC
7	Isolador ômega pinheiro 150kV	PC
8	Isolador ômega pinheiro 150kV	PC
9	Curva 135 graus PVC rosqueável ou cabeçote	PC
10	Luva PVC rosqueável 2 1/2"	PC
11	Armação de aço zincado n 12 BV6	n

PLANTA DE LOCAÇÃO 01
ÁREA CERCADA = 546,81 m²
PERÍMETRO = 105,12
ESCALA 1:75

DEM DO POSTE AUXILIAR
10/150

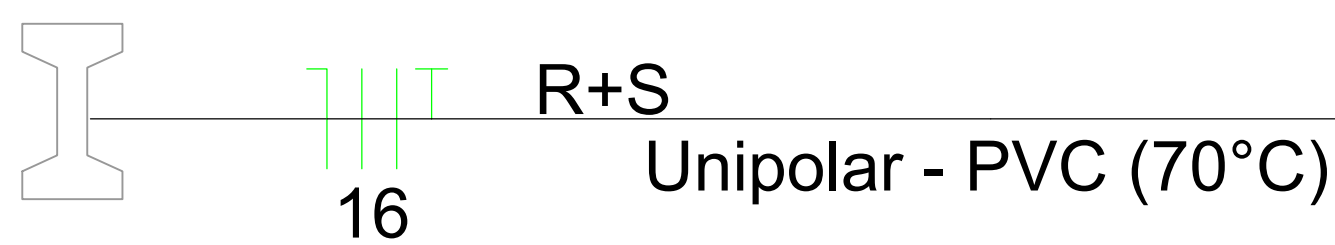

10	Isolado - PVC (70°C)	(8085 W)	R+S	(UBS)
10	Isolado - PVC (70°C)	(15140 W)	R+S	(ALOJAMENTO)
10	Isolado - PVC (70°C)		R+S	(GERADOR)
1.5	Isolado - PVC (70°C)	(192 W)	R	(ILUMINAÇÃO)

13

REQUERENTE

GSS CONTRUÇÕES

LOCAL

ALDEIA MURUTU

DESCRIÇÃO

PROJETO SISTEMA DE LIGAÇÃO COM CHAVE DE TRANSFERENCIA GERADOR

CONTEUDO

PROJETO ELETRICO DE LOGISTICA DE COMANDO

RESPONSÁVEL

ELETRIC SERVIÇOS ENG.

DESENHO

RUAN LASTRINE

ESCALA

SEM ESCALA

CREA

89313135272

DATA

Electric Services Engenharia
CNPJ 58.165.764/0001-17