

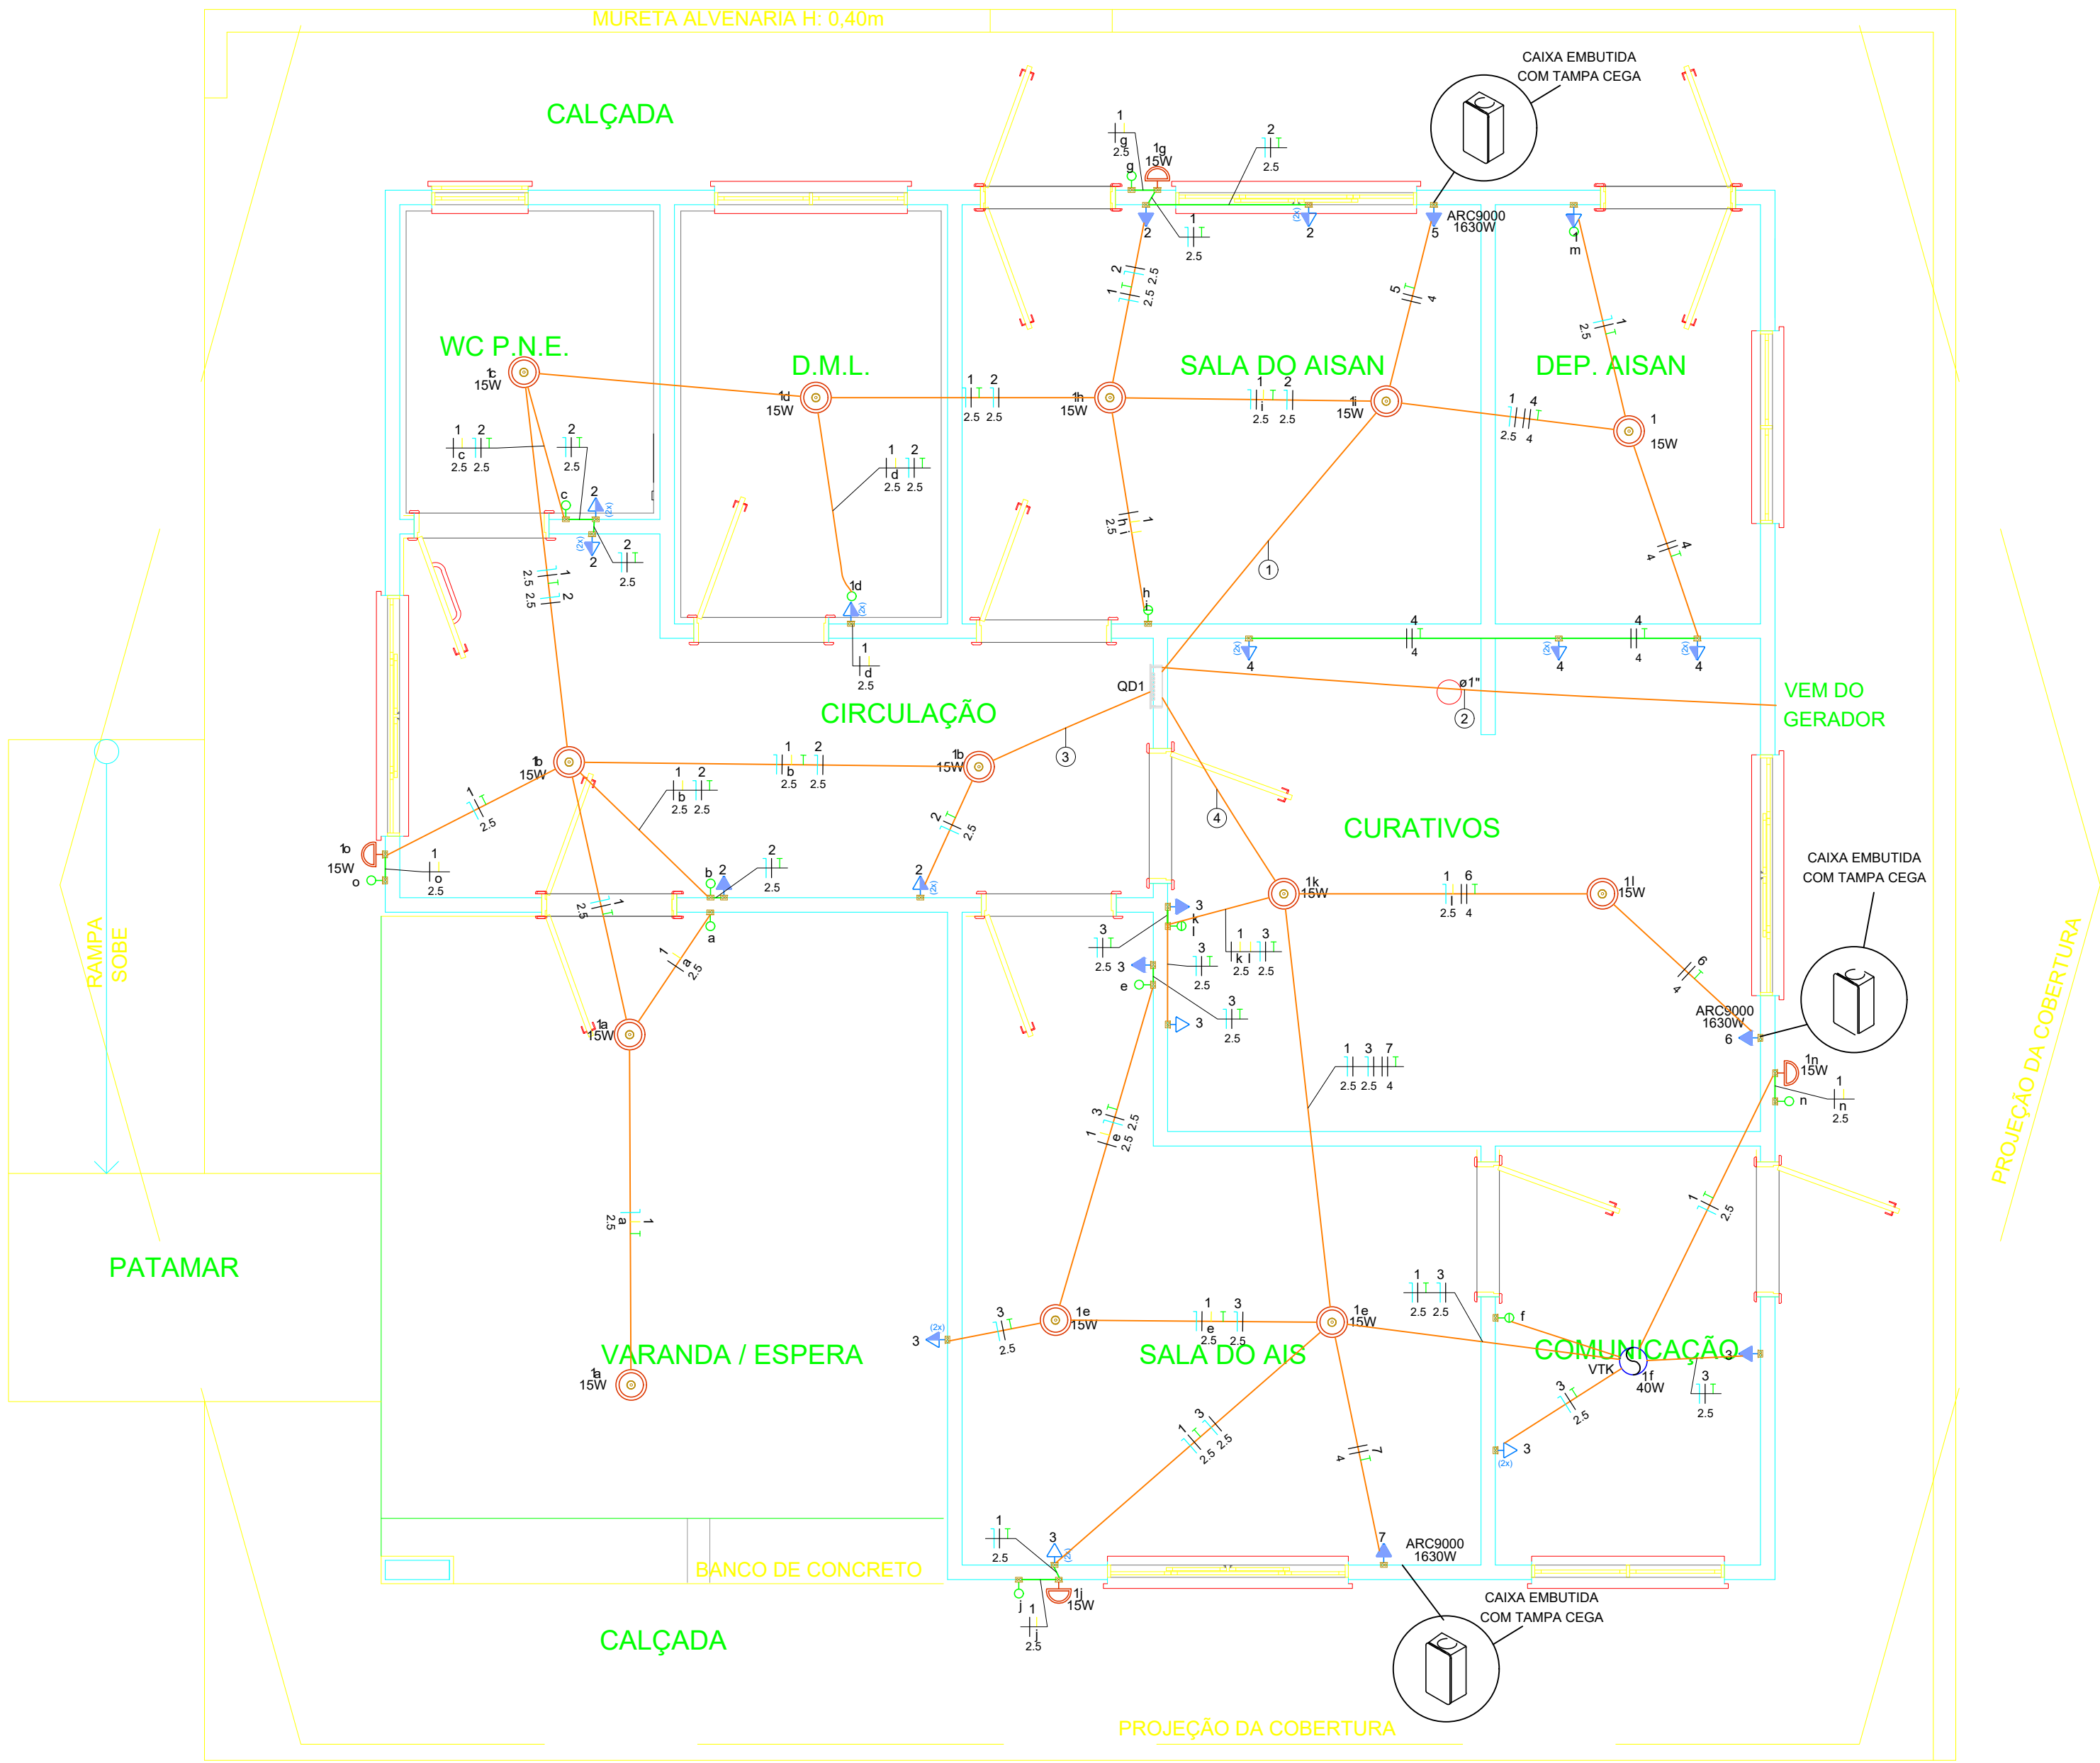
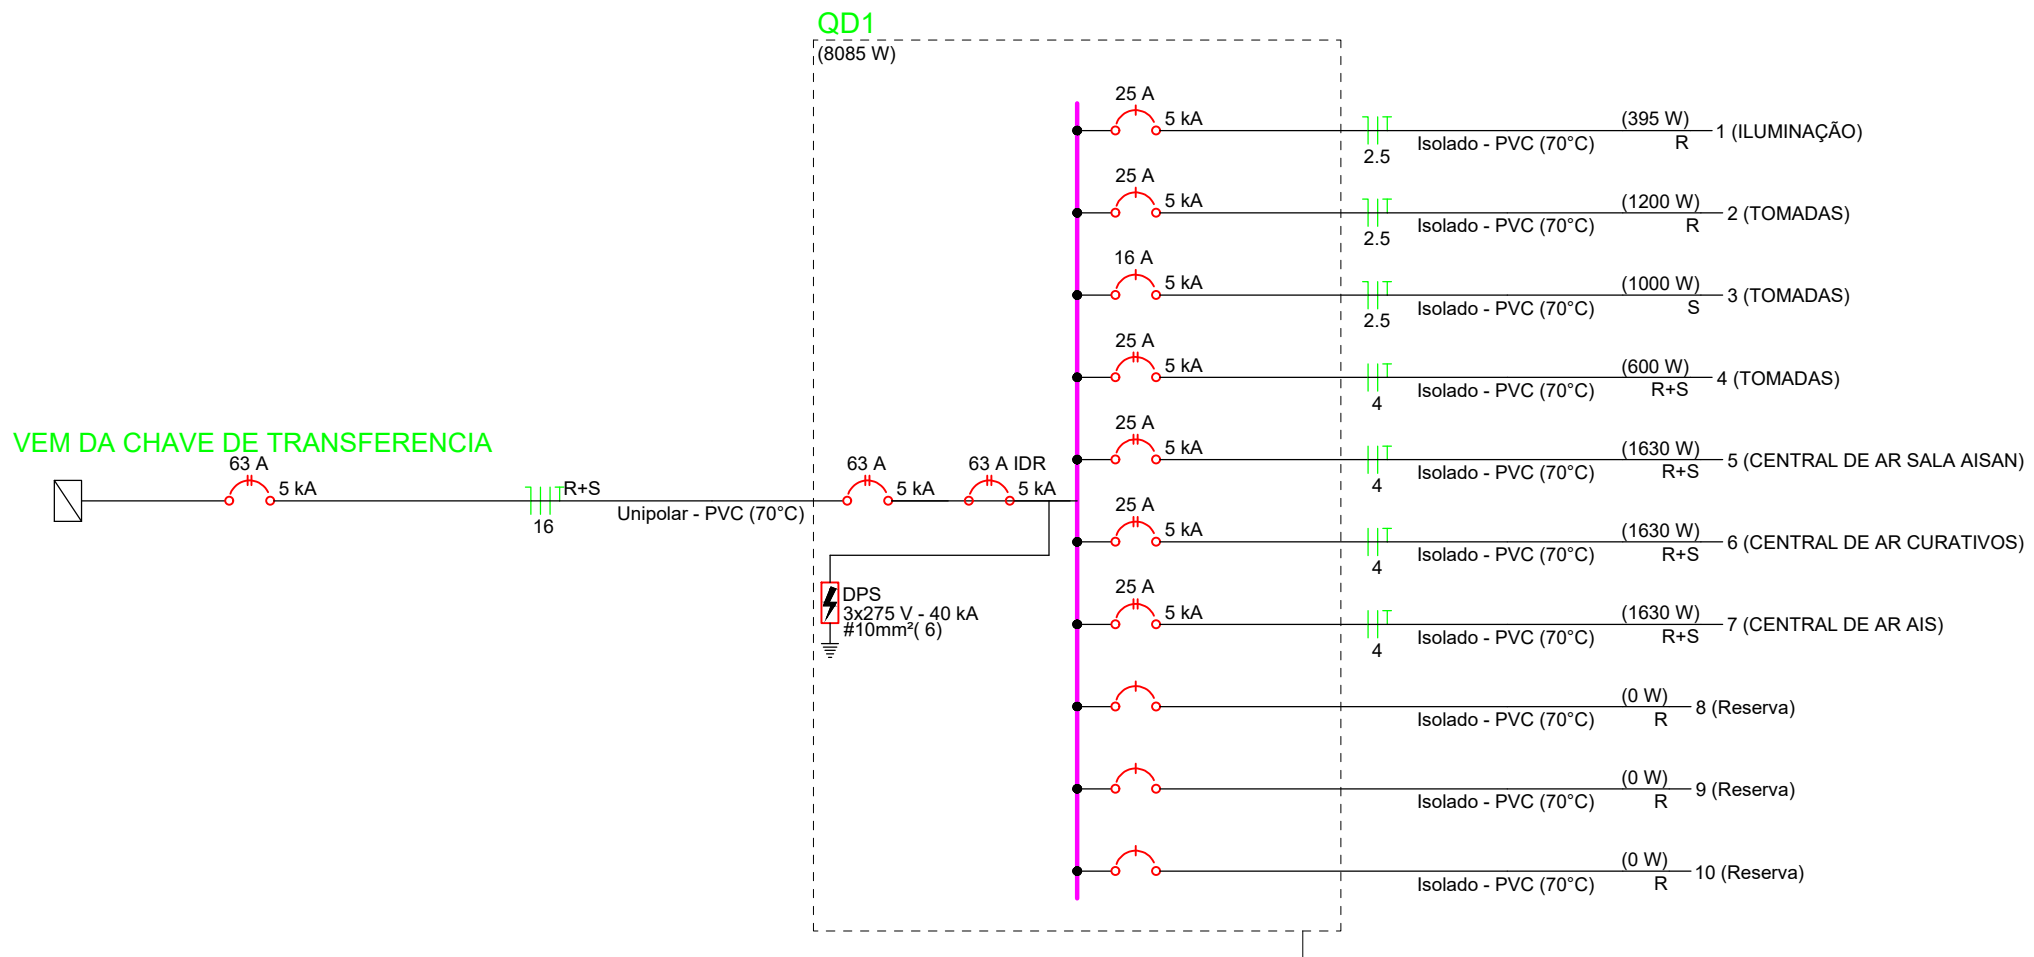
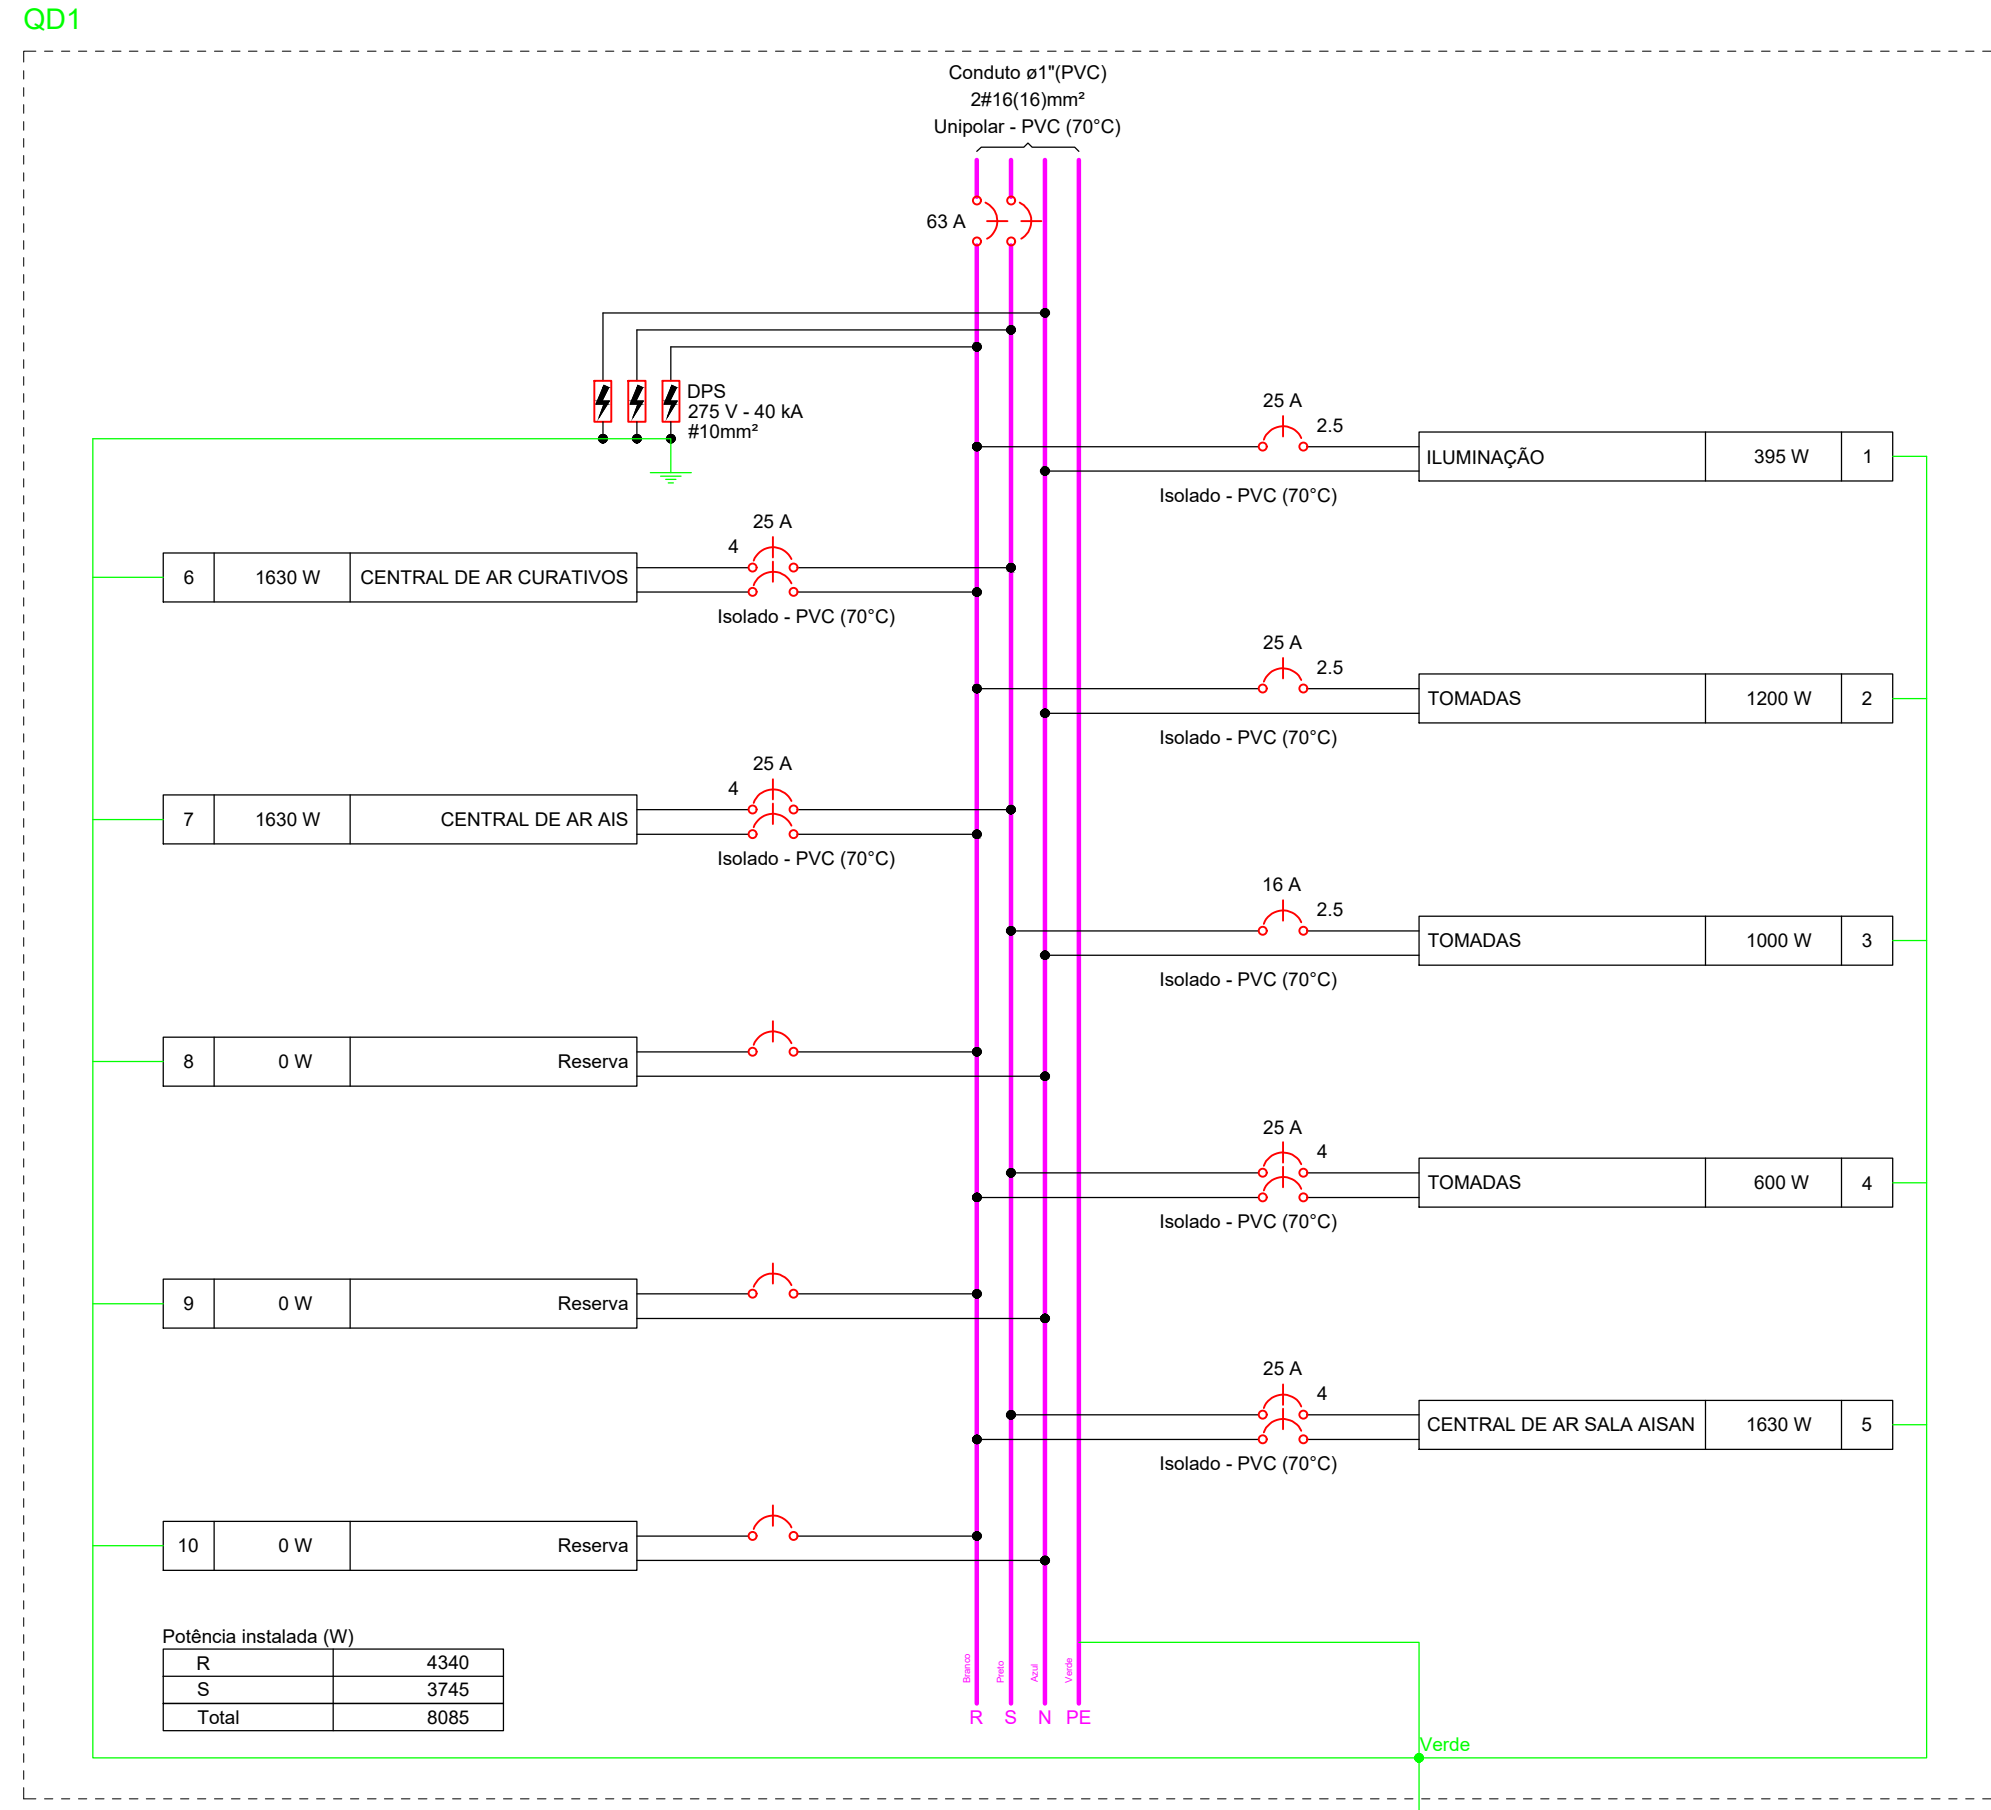


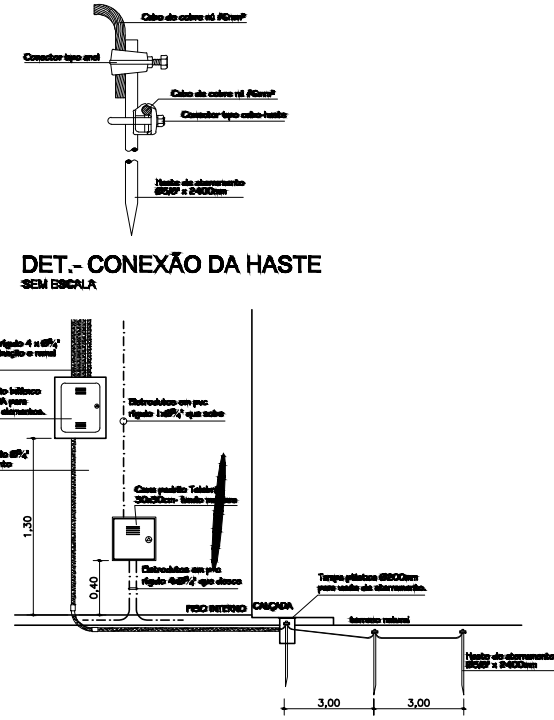

		Quadro de Cargas (QD1) - UBS																						
Circuito	Descrição	Esquema	Método de inst.	Tensão (V)	Iluminação (W)	Tomadas (W)	Pot. total (W)	Pot. - R (W)	Pot. - S (W)	Pot. - T (W)	FCT	FCA	In' (A)	Ip' (A)	Seção (mm²)	Ic (A)	Icc (kA)	dV par (%)	dV total (%)					
1	ILUMINAÇÃO	F+N+T	B1	127 V	17	1	406	395	R	395	1	1.00	0.70	2.1	3.2	2.5	24.0	5	25	0.14	1.35			
2	TOMADAS	F+N+T	B1	127 V		12	1333	1200	R	1200		1.00	0.80	7.7	10.5	2.5	24.0	5	25	0.79	2.00			
3	TOMADAS	F+N+T	B1	127 V		10	1111	1000	S		1000		1.00	0.70	12.5	8.7	2.5	24.0	5	16	0.97	2.18		
4	TOMADAS	F+F+T	B1	220 V		6	667	600	R+S	300	300	1.00	0.80	3.8	3.0	4	32.0	5	25	0.18	1.39			
5	CENTRAL DE AR SALA AISAN	F+F+T	B1	220 V		1	1811	1630	R+S	815	815	1.00	0.80	10.3	8.2	4	32.0	5	25	0.30	1.51			
6	CENTRAL DE AR CURATIVOS	F+F+T	B1	220 V		1	1811	1630	R+S	815	815	1.00	0.70	11.8	8.2	4	32.0	5	25	0.37	1.58			
7	CENTRAL DE AR AIS	F+N+T	B1	220 V		1	1811	1630	R+S	815	815	1.00	0.70	11.8	8.2	4	32.0	5	25	0.42	1.63			
8	Reserva	F+N+T	B1	127 V			0	0	R			1.00	1.00	0.0	0.0	1.5	17.5	5	15	0.00	0.00			
9	Reserva	F+N+T	B1	127 V			0	0	R			1.00	1.00	0.0	0.0	1.5	17.5	5	15	0.00	0.00			
10	Reserva	F+N+T	B1	127 V			0	0	R			1.00	1.00	0.0	0.0	1.5	17.5	5	15	0.00	0.00			
TOTAL					17	1	29	3	8951	8085	R+S	4340	3745	0										

Quadro de Demanda (QD1) - UBS			
Tipo de carga	Potência instalada (kVA)	Fator de demanda (%)	Demanda (kVA)
Iluminação Condomínio (Residencial)	1.52	100.00	1.52
Tomadas condomínio (Residencial)	1.33	20.00	0.27
Uso Específico	6.10	100.00	6.10
TOTAL			7.88

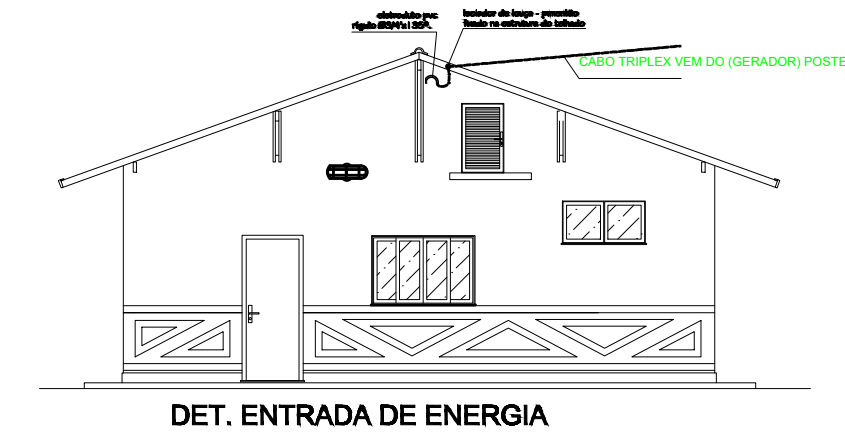

Legenda - Pavimento	
Elétrica	Teto
	Média
Legenda de fiação - Pavimento	
1	1 2 4 5 2.5 2.5 4 4
2	VEM DO GERADOR
3	1 2 2.5 2.5
4	1 3 6 7 2.5 2.5 4 4

3
3

REQUERENTE	GSS CONTRUÇÕES
LOCAL	ALDEIA MURUTU
DESCRIÇÃO	REFORMA DA UBS
CONTEUDO	DIMENSIONAMENTO ELÉTRICO

RESPONSÁVEL	ELETRIC SERVIÇOS ENG.
DESENHO	RUAN LASTRINE
ESCALA	SEM ESCALA

CREA	89313135272
DATA	

