
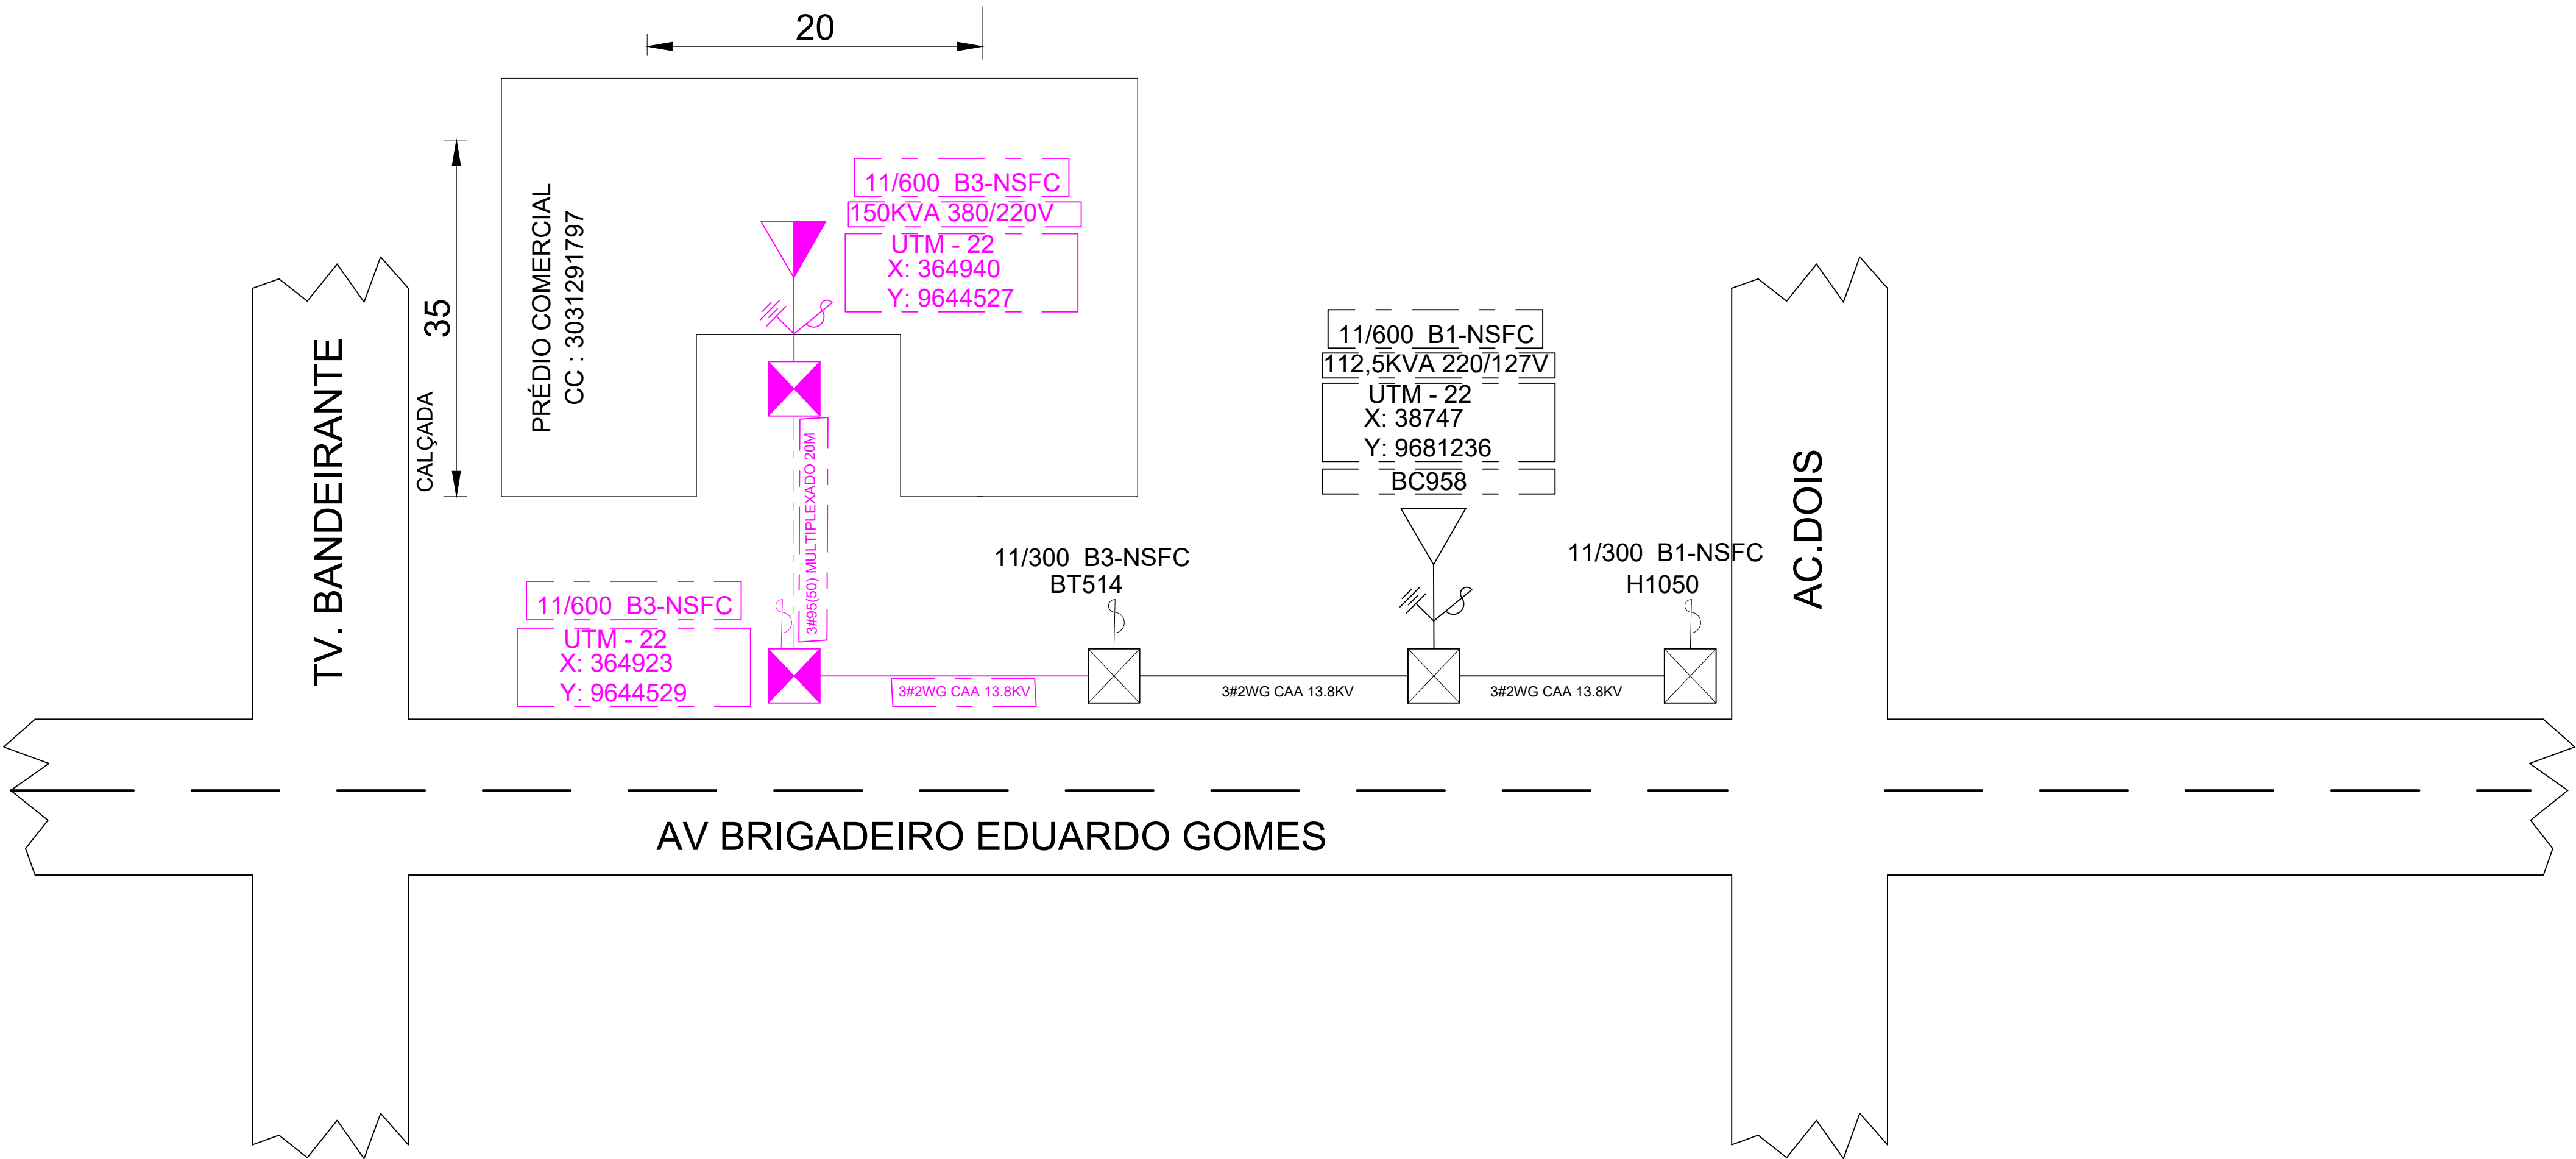
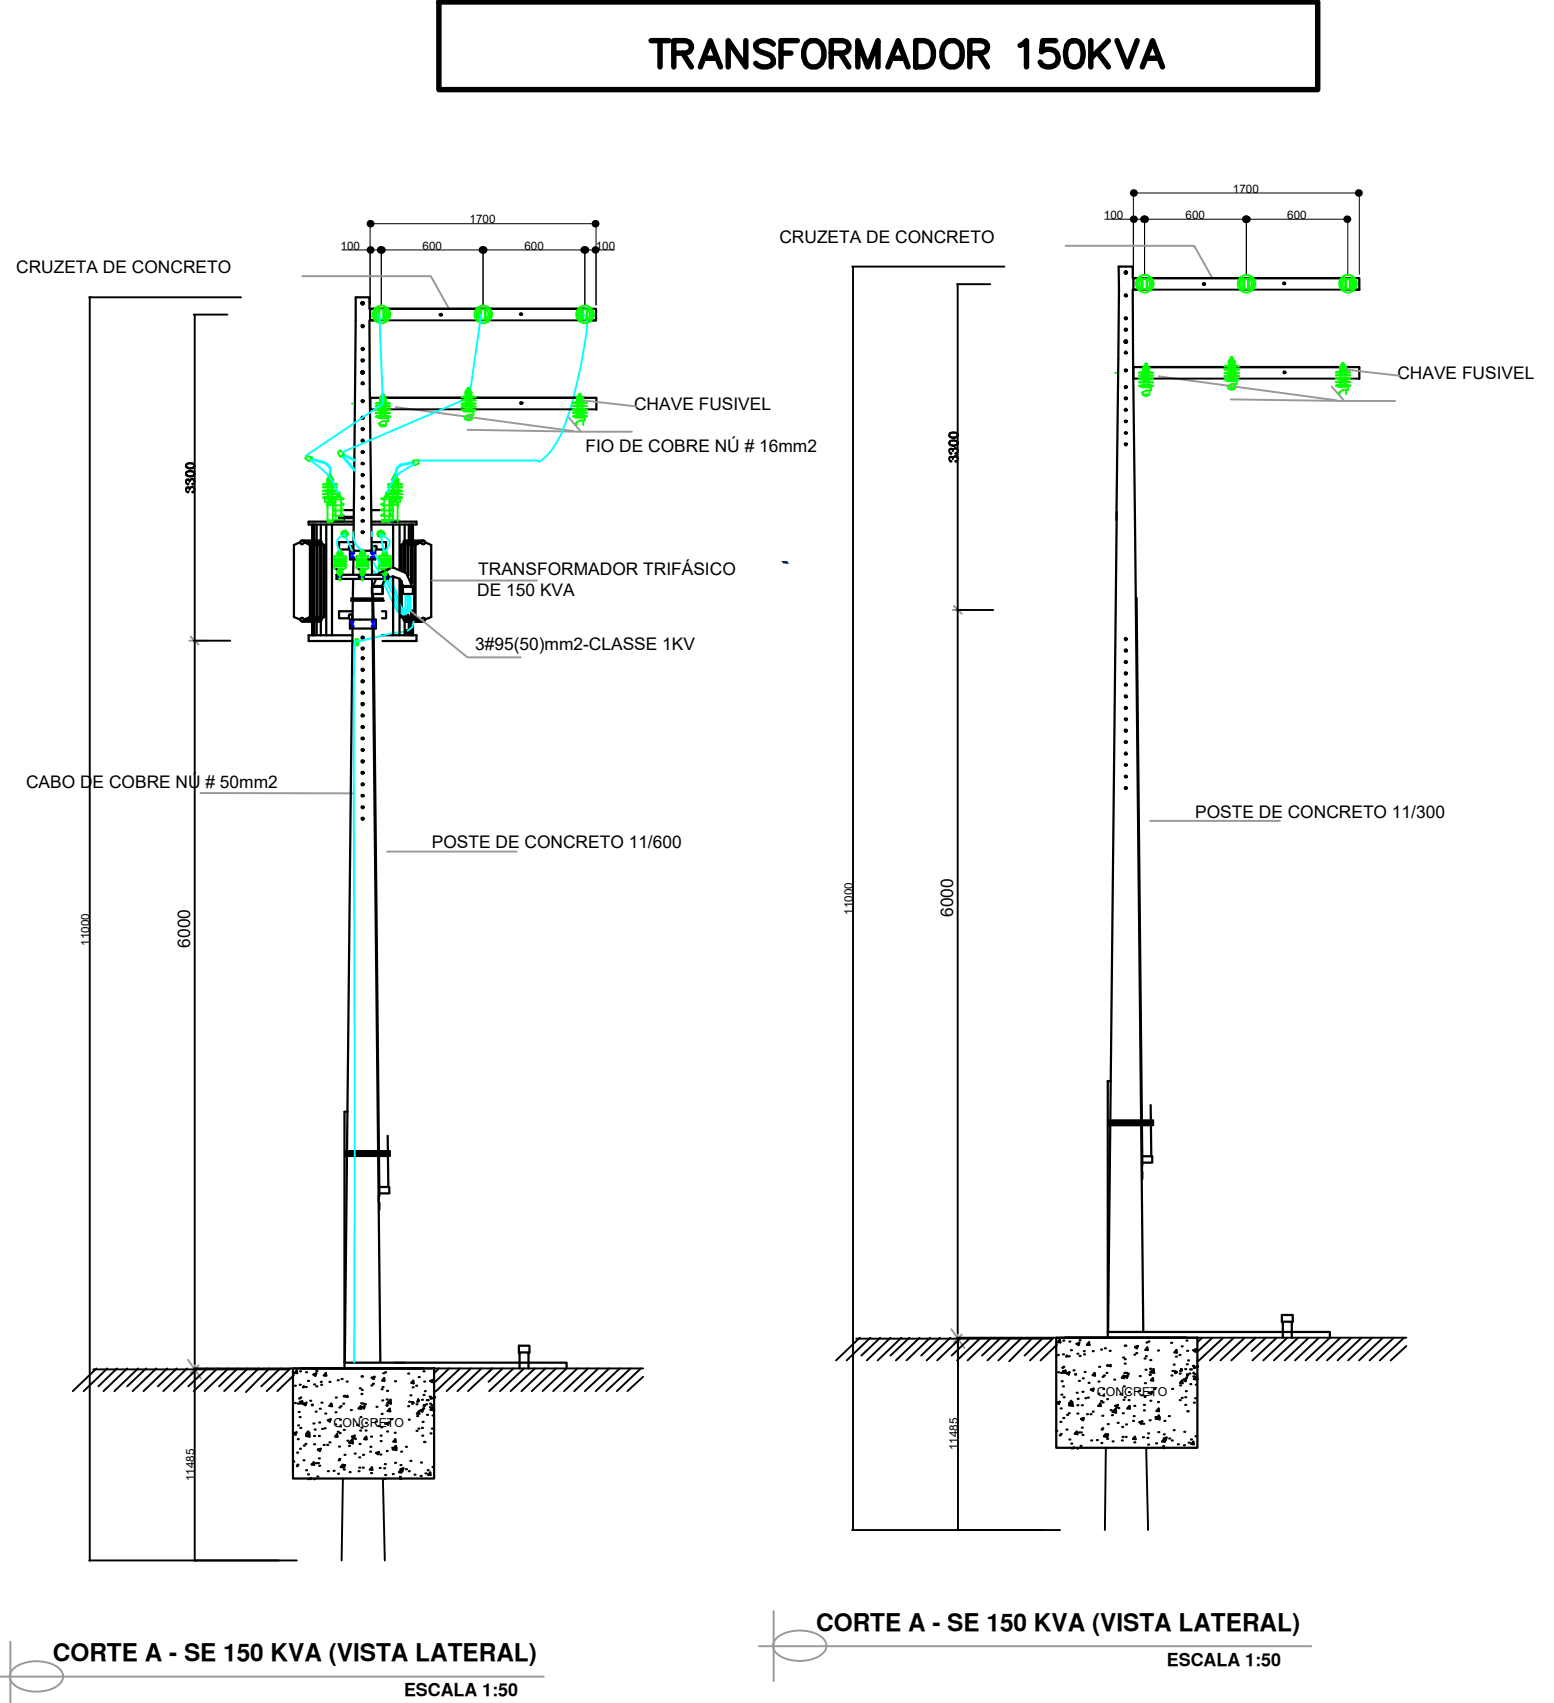
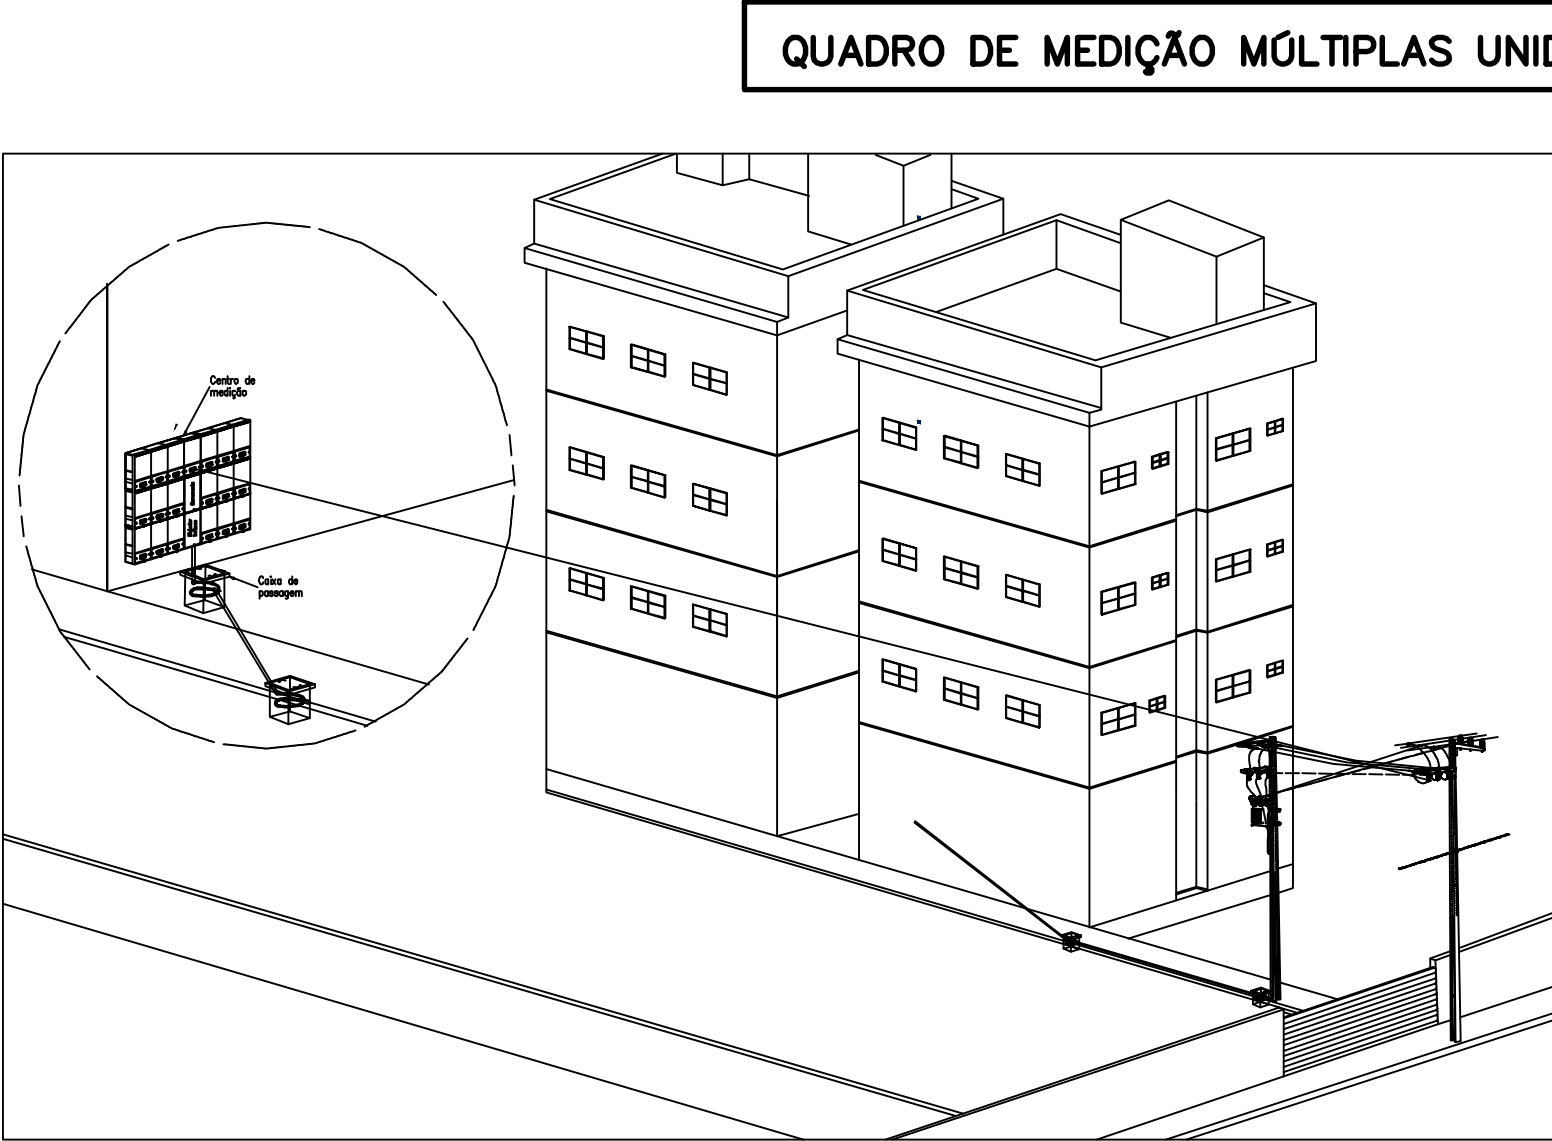


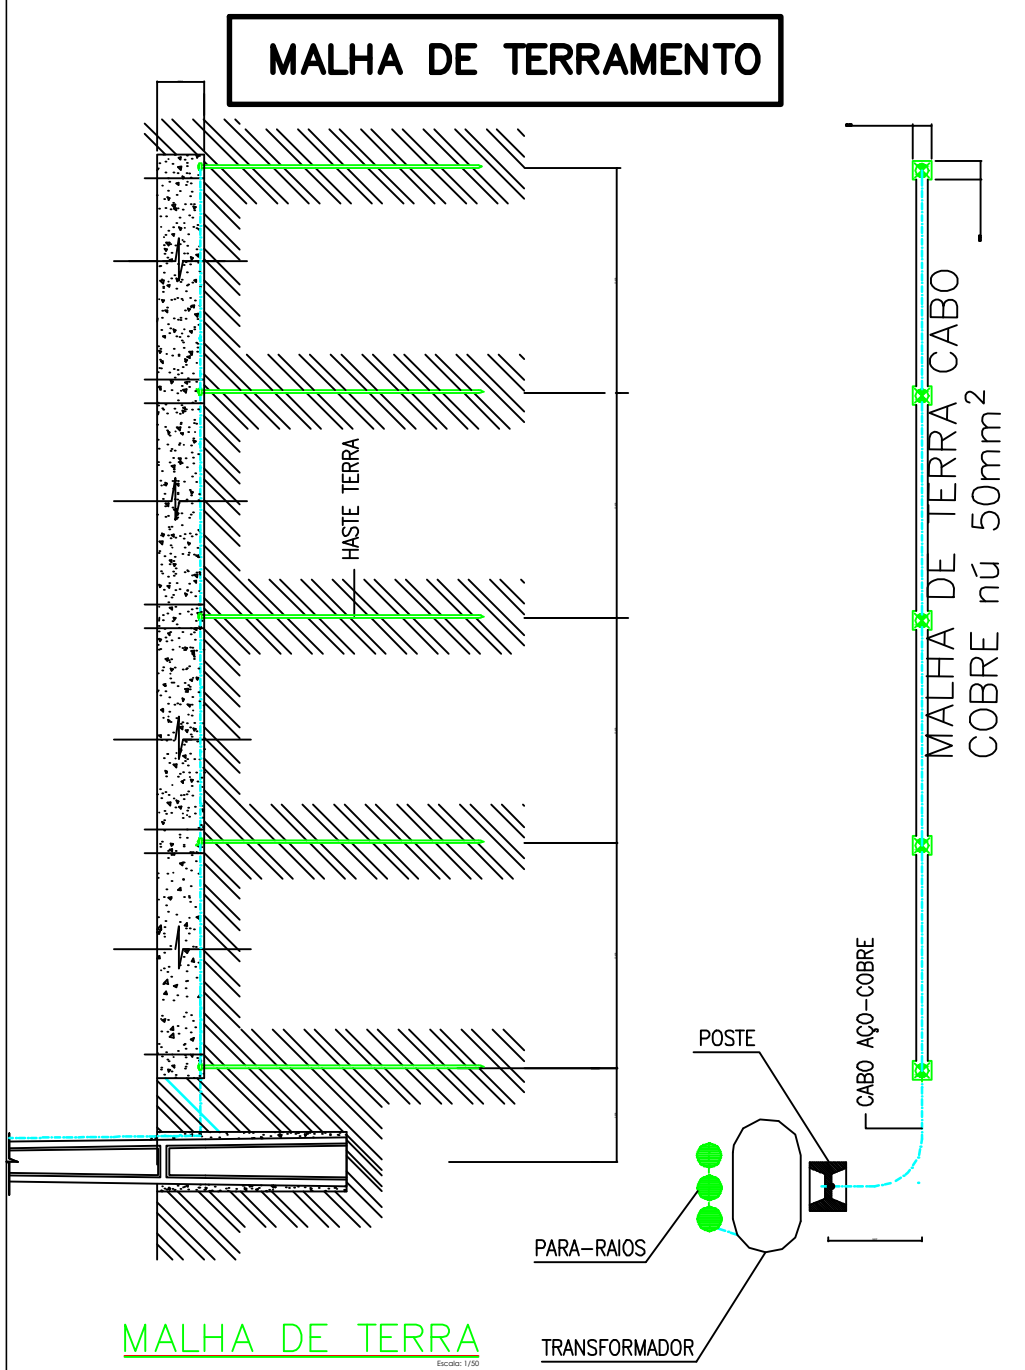

ITEM	SIMBOLOGIA	DESCRIÇÃO
01		POSTE DT EXISTENTE
01		POSTE DT PROJETADO
01		TRANSFORMADOR PROJETADO
01		ATERRAMENTO
01		CHAVE FUSIVEL
01	C0000000	N° DE IDENTIFICAÇÃO DO POSTE
01		REDE NUA EXISTENTE 3# 2AWG CAA 13.8KV
01		REDE NUA PROJETADA 3# 2AWG CAA 13.8KV
01		REDE MULTIPLEXADA PROJETADA 3#70(35)

- Alça Pré-formada Para Cabo de Alumínio
- Isoladores de Ancoragem 15KV
- Gancho Othal, Parafuso Cabeça Quadrada e Parafuso Othal Ø 16 x 400mm
- Cruzeta de Fibra de Vidro Tipo "L", 1.700mm
- Para-raios Oxi-do de Zinco 12 KV, 10 kA para 13.8 Kv
- Transformador de Distribuição 15 KV - Buchas de 150KV, para Rede de 13.8
- Cabo de Cobre Isolado XLPE 90° - EPR 90° ou HEPR 90° - Isolamento 0,6/1kV -
- Supporte de Transformador Tipo Cantoneira
- Cappotele conforme tabelas 11 ou 11A de Aço Galvanizado a fogo (até 2 km da Orla Marítima Utilizar Curva em PVC)
- Eletroduto conforme tabelas 11 ou 11A de Aço Galvanizado a fogo da Orla Marítima Utilizar Eletroduto em PVC
- Cabo de Cobre (ou Aço Cobreado) nu 50 mm² - Aterramento
- Arame de Aço Galvanizado 12BVG
- Poste Concreto Armado DT 11m600da para Transformadores até 150 kVA
- Caixa de Medição para Transformador de 75 a 150 kVA
- Caixa de Inspeção do Aterramento

1
1

REQUERENTE	GSS CONTRUÇÕES
LOCAL	AVENIDA BRIGADEIRO EDUARDO GOMES S/N, Bairro do (a) EXPLANADA DO XINGU
DESCRIÇÃO	PROJETO DE DIMENSIONAMENTO ELETRICO MT
CONTEÚDO	PROJETO ELETRICO SUBESTAÇÃO AEREO 150KVA GEORREFERENCIA

RESPONSÁVEL	REGISTRO
	89313135272
	DATA
	04/03/2026
DESENHO	RUAN LASTRINE
ESCALA	SEM ESCALA

Electric Services Engenharia
CNPJ: 08.000.741/0001-17

