


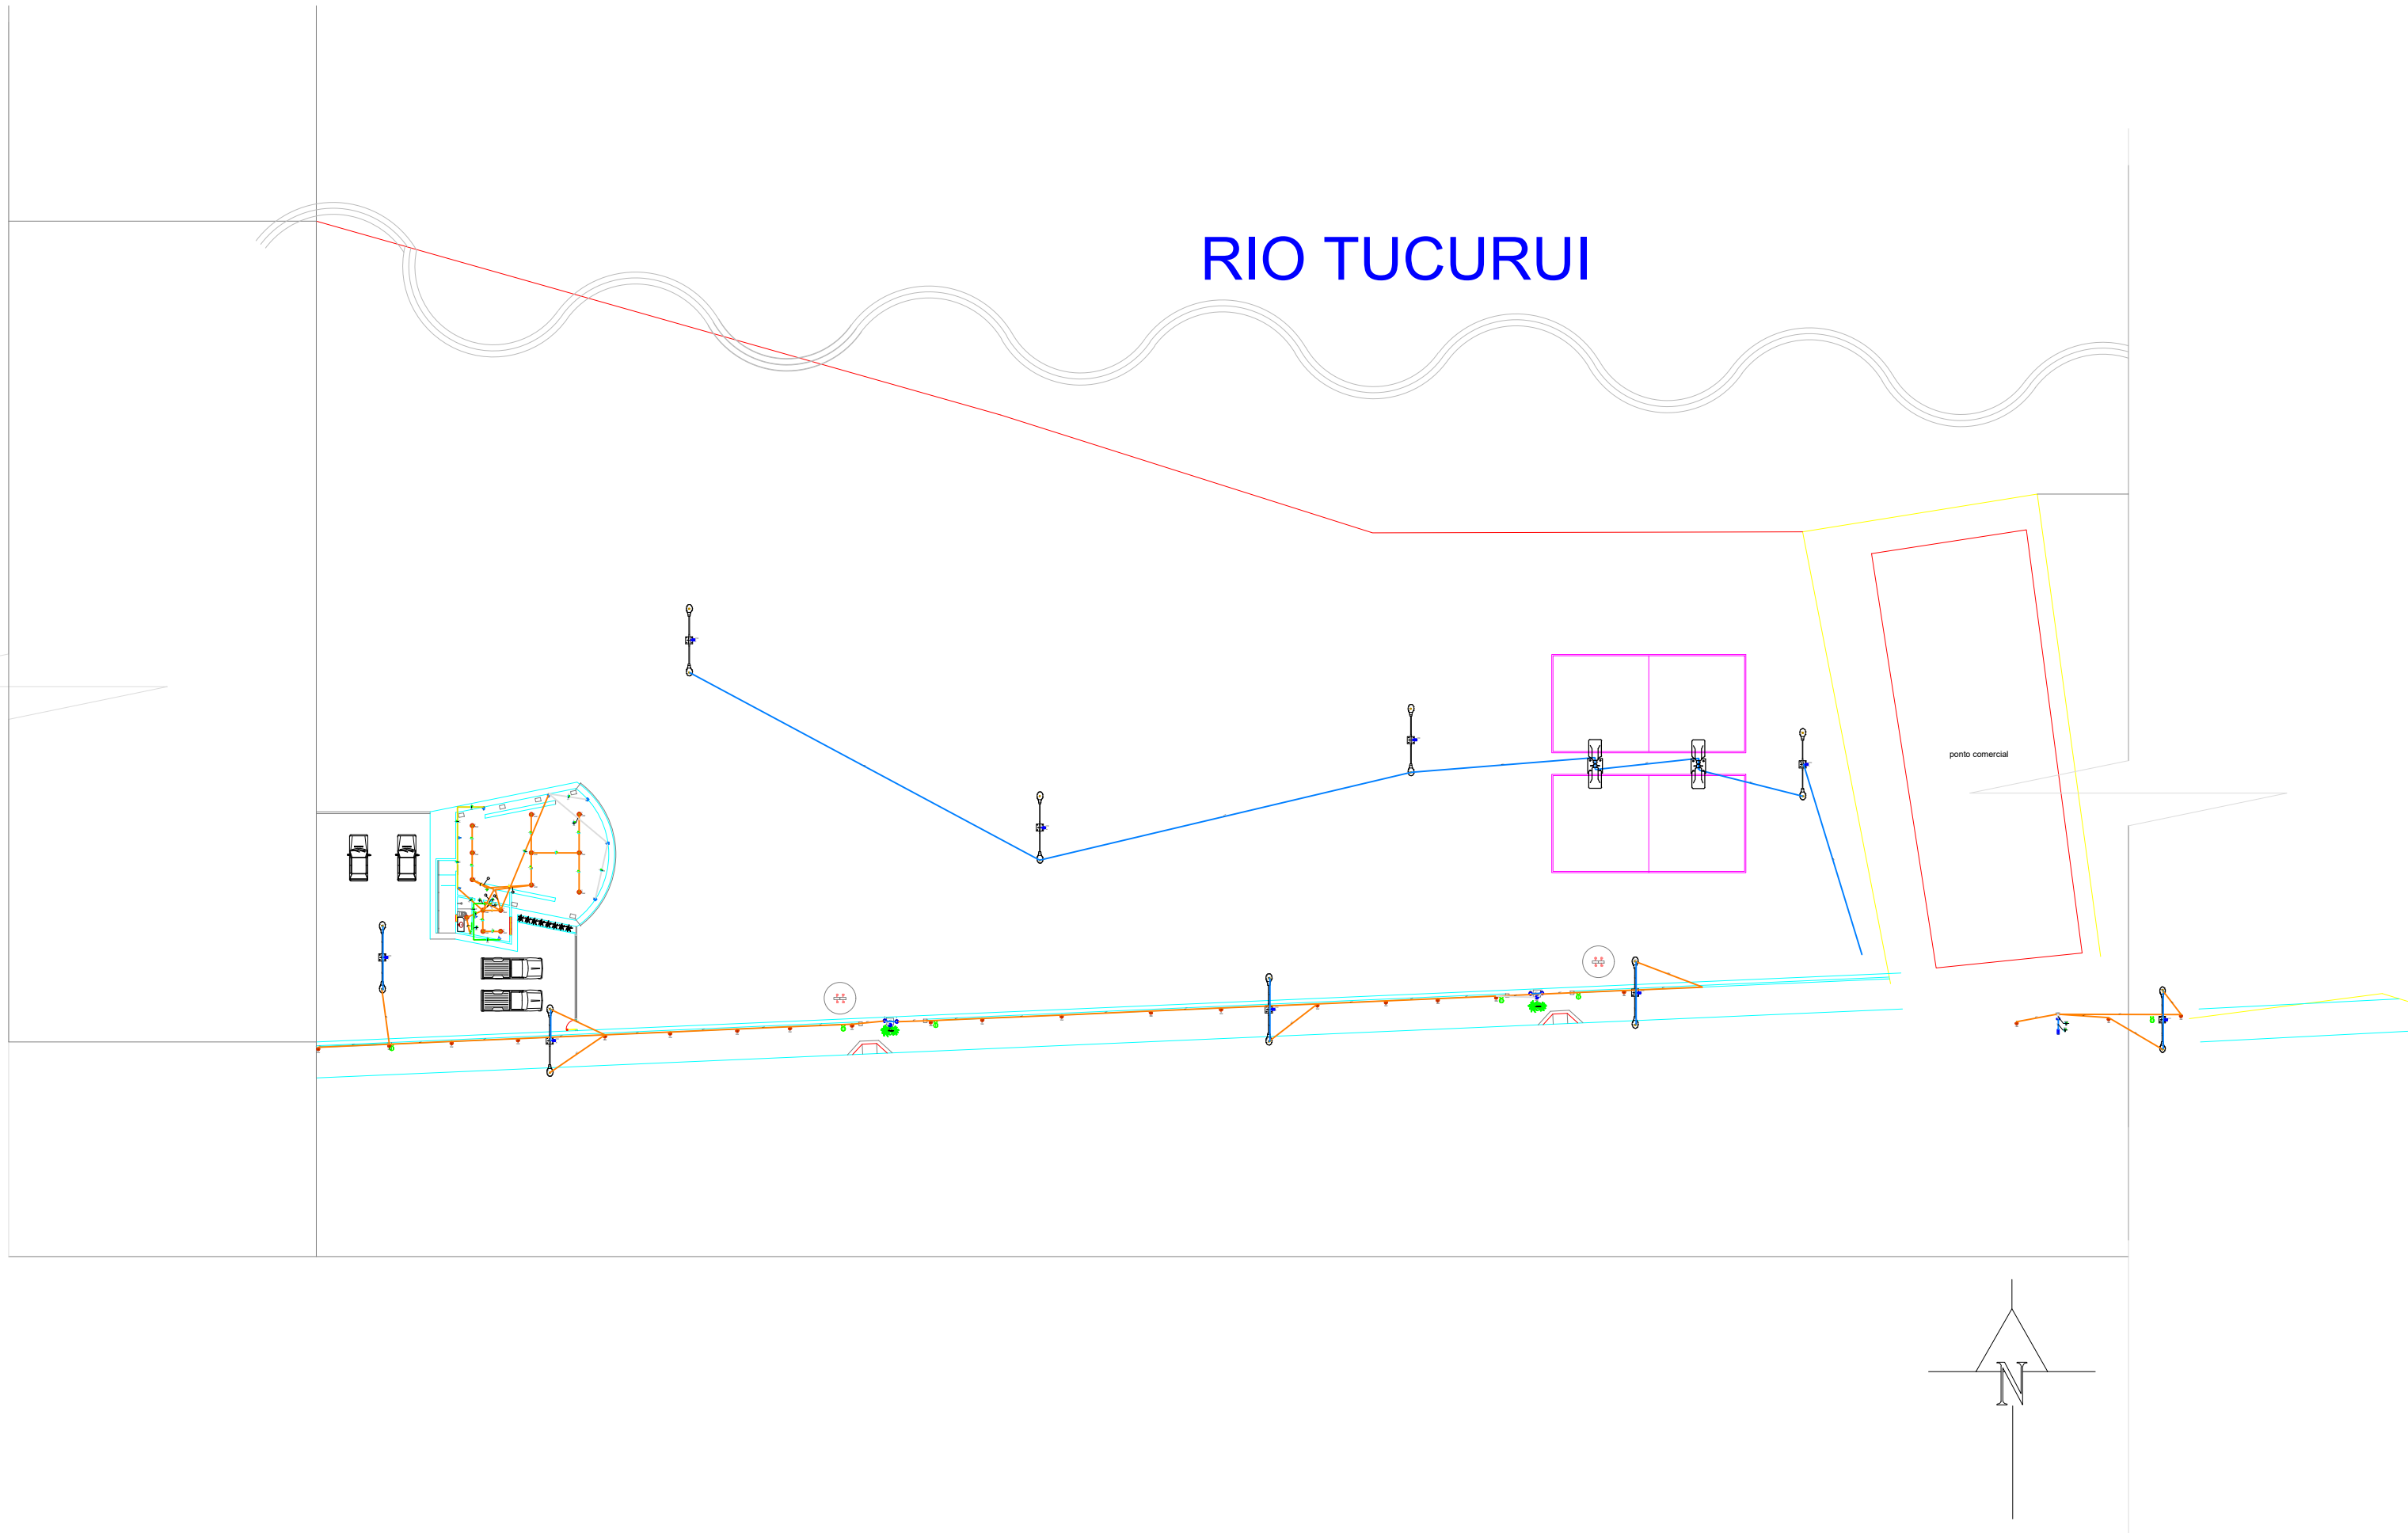
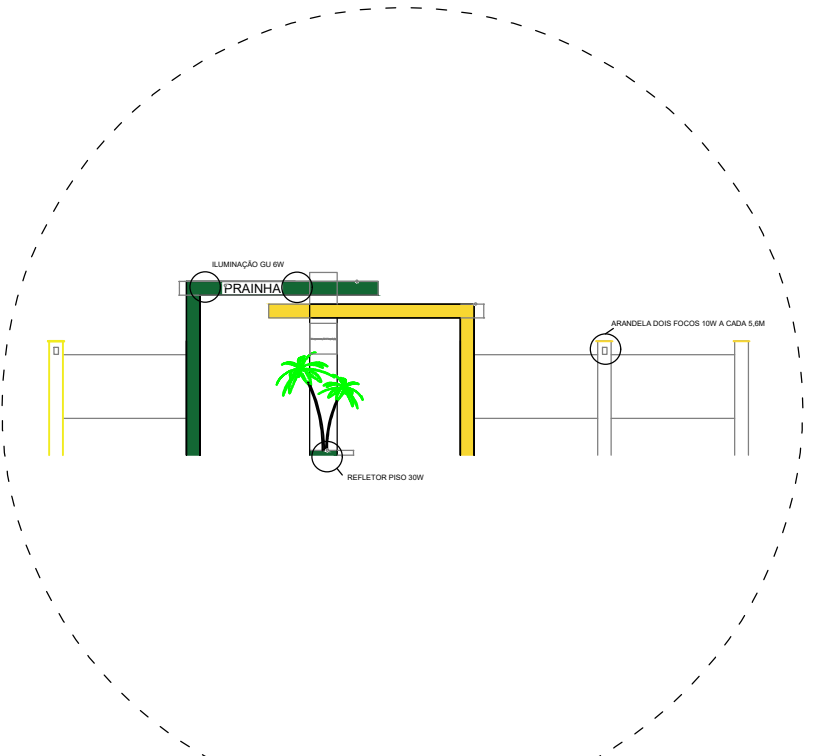


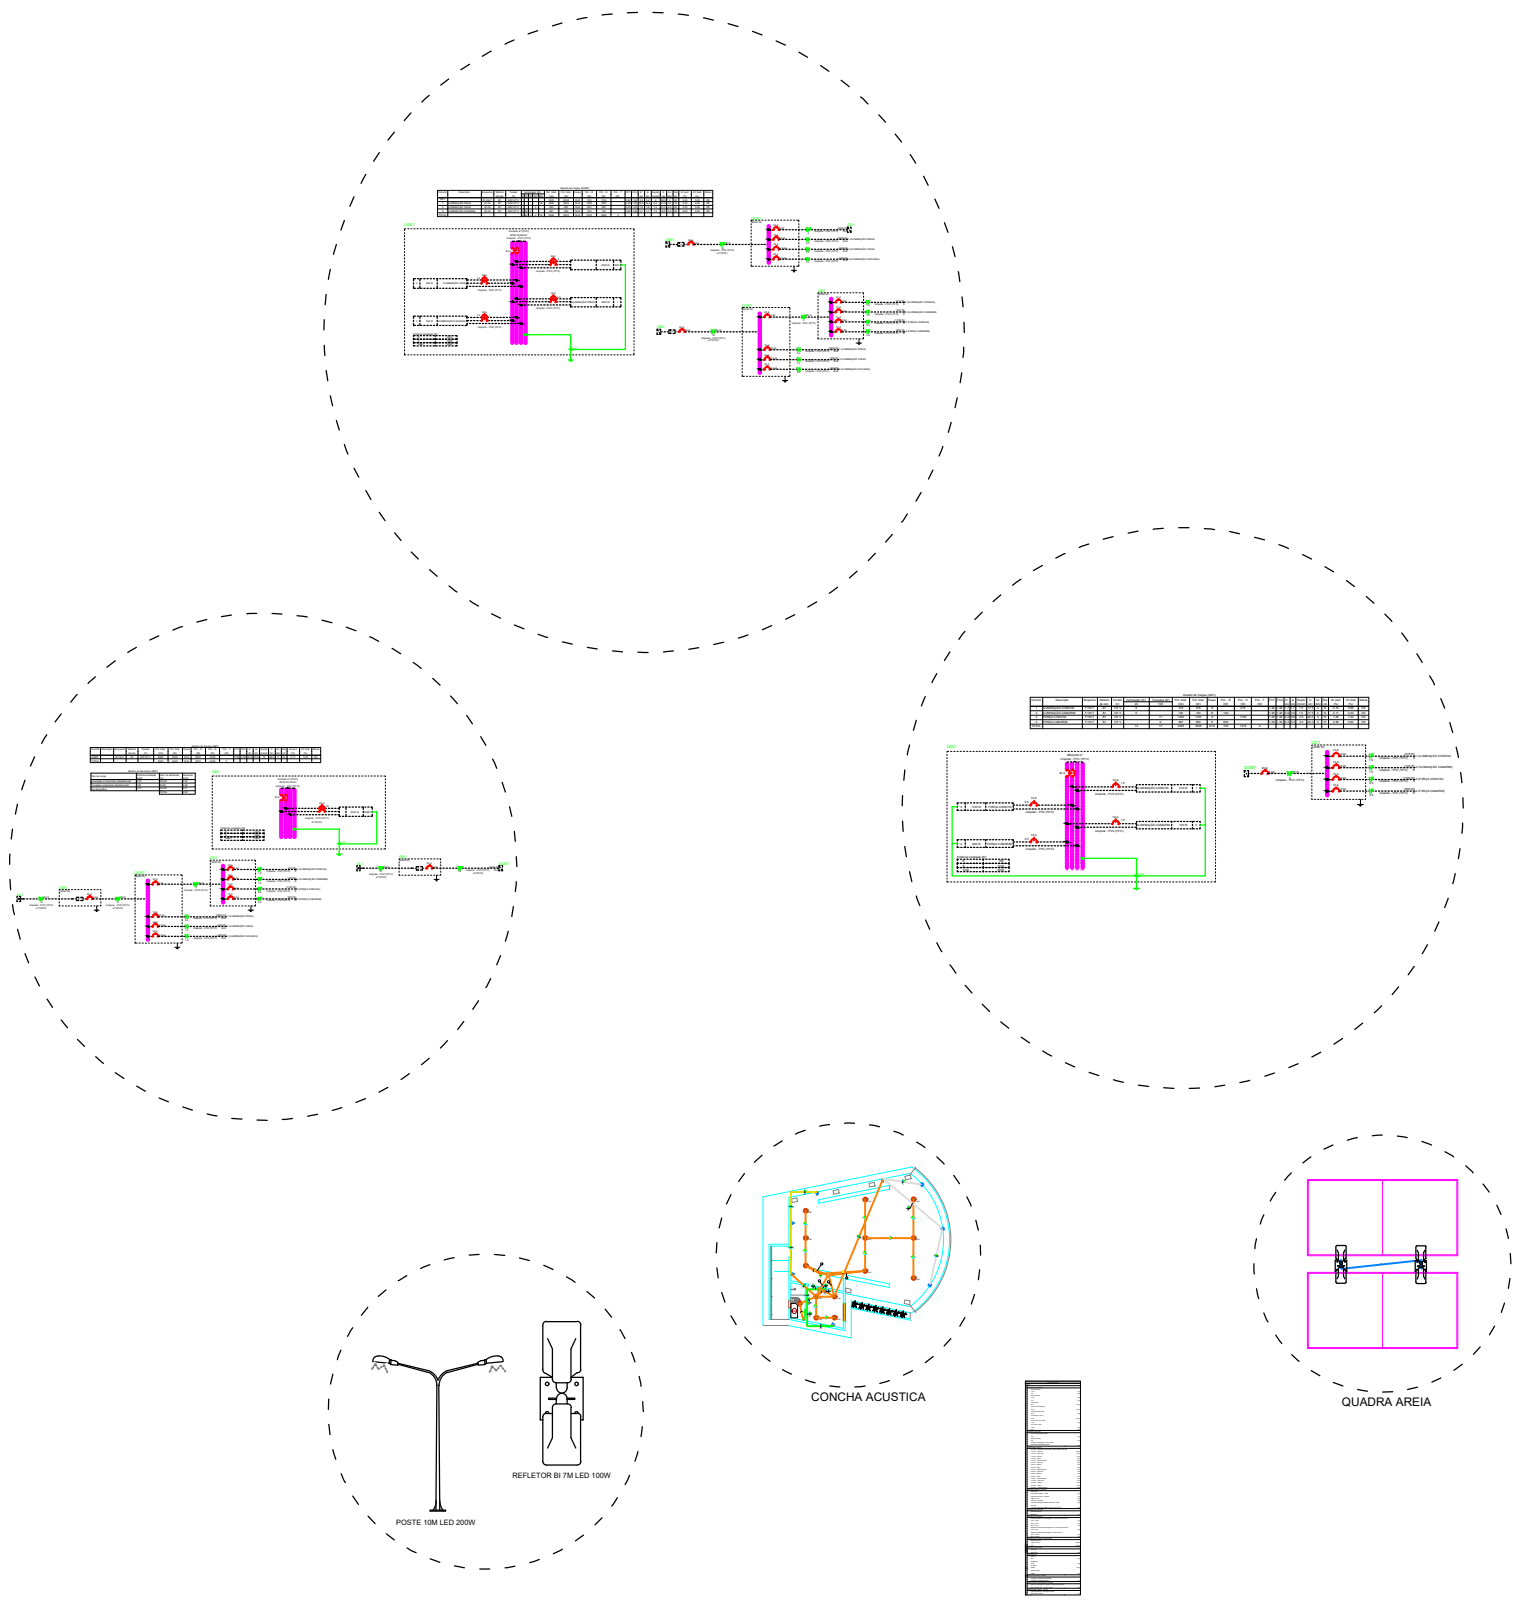

- NOTA
- POSTE NA AREIA COM ALTURA DE 7M
 - POSTE NA CALÇADA COM ALTURA DE 10M
 - FORMA DE ALIMENTAÇÃO DE POSTES CABO TRIPLEX
 - INSTALAÇÃO DA FACHADA EMBUTIDA
 - ALIMENTAÇÃO DO BH INDICADO SERA REPETIDO CONFORME O EXEMPLO NO CORTE
 - ALIMENTAÇÃO DA CONCHA ACUSTICA SERA FEITA PELO POSTE MAIS PROXIMO
 - ALIMENTAÇÃO DA CONCHA ACUSTICA SERA FEITA PELO POSTE MAIS PROXIMO

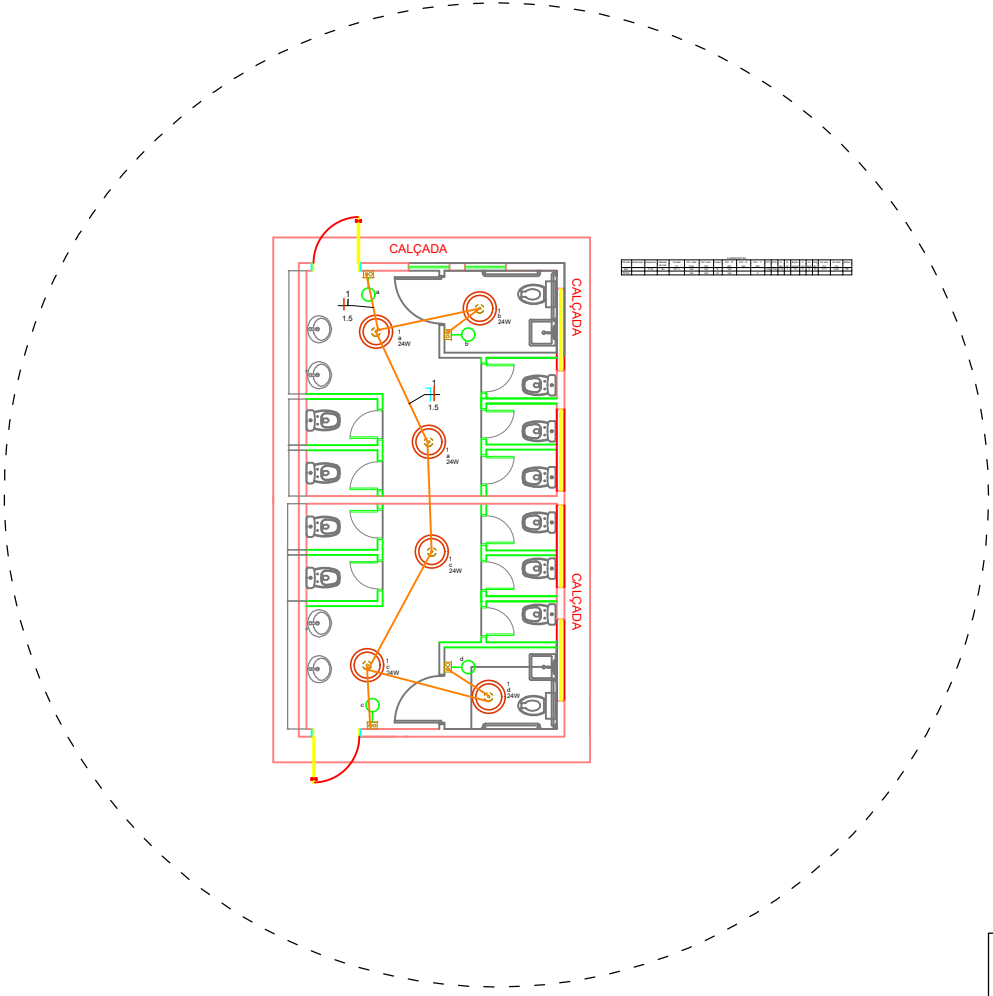

ILUMINAÇÃO DA FACHADA

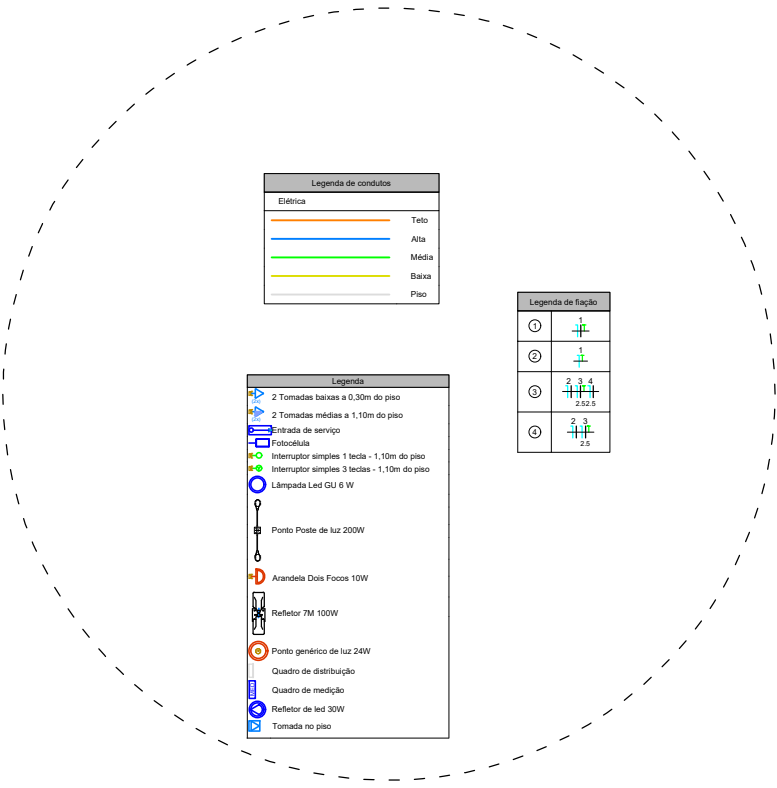

1 1	REQUERENTE LUMEN ENGENHARIA	RESPONSÁVEL ELETRIC SERVIÇOS ENG.	CREA 89313135272	
	LOCAL PRAIA ARTIFICIAL		DATA	
	DESCRIÇÃO PROJETO ELETRICO - DIMENSIONAMENTO DE CIRCUITOS NA PRAIA ARTIFICIAL	DESENHO RUAN LASTRINE		
	CONTEÚDO PROJETO ELETRICO DE CIRCUITOS	ESCALA SEM ESCALA		