
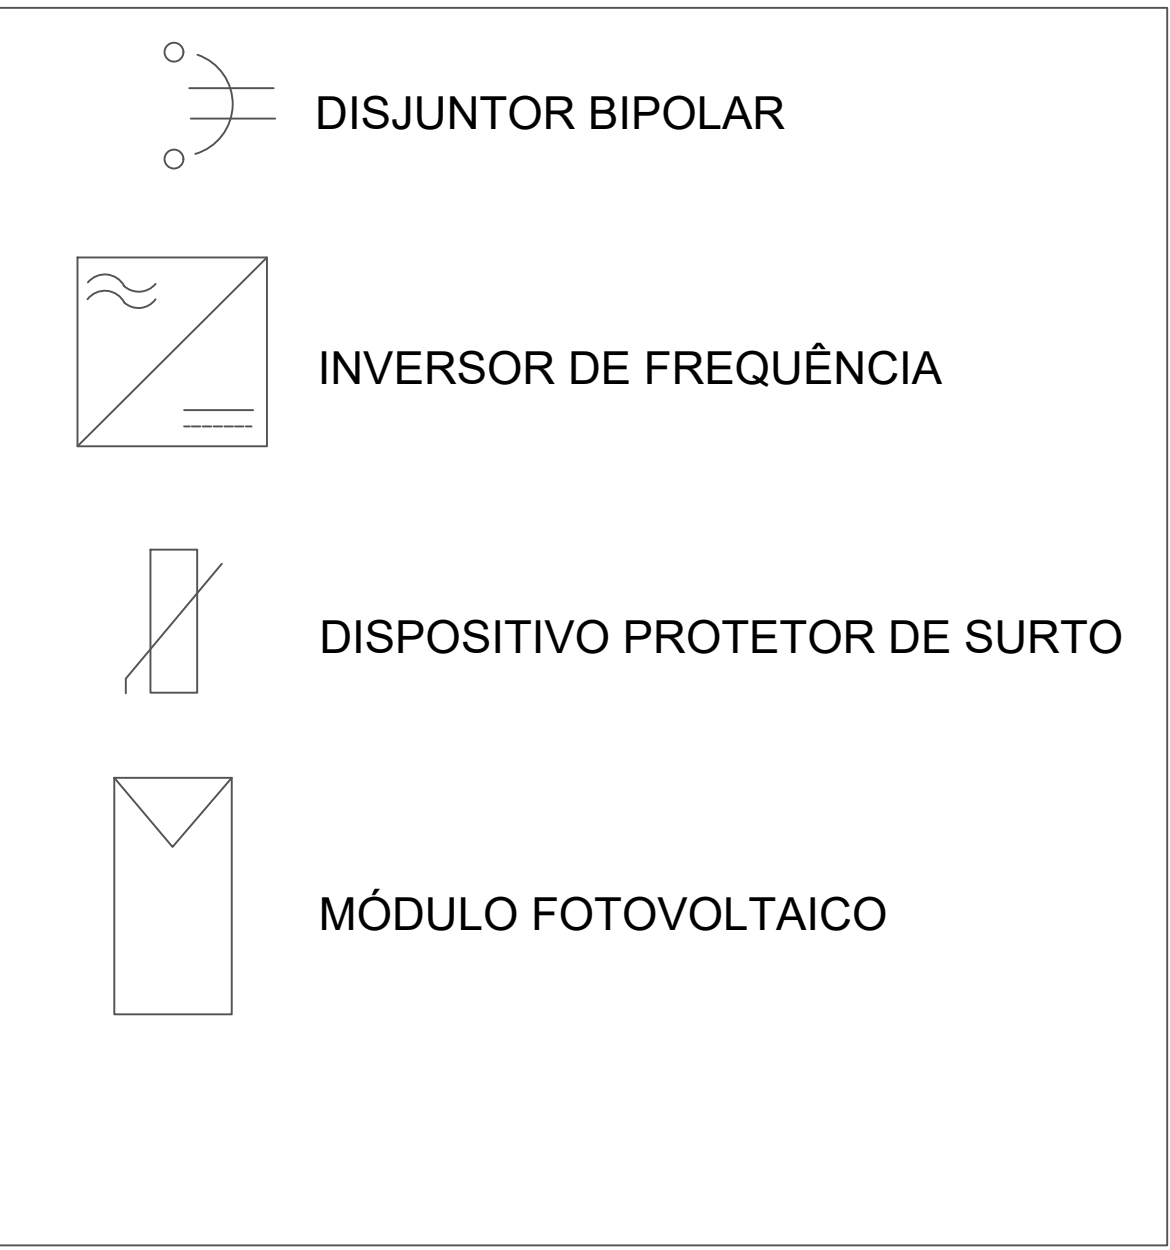
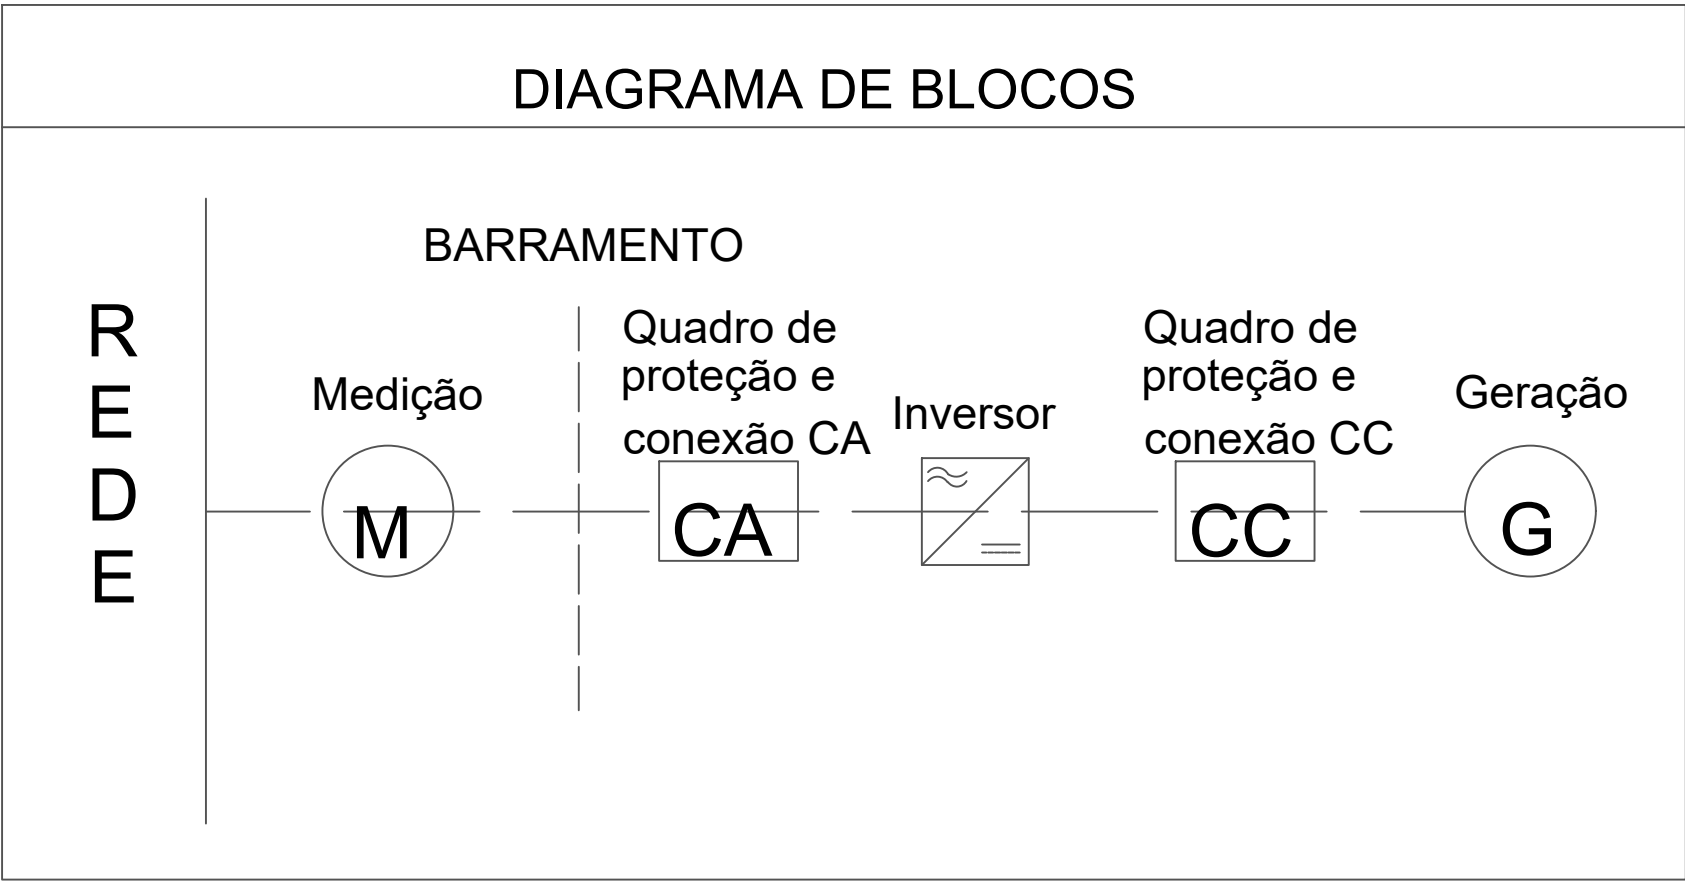


DIAGRAMA UNIFILAR - BLOCOS

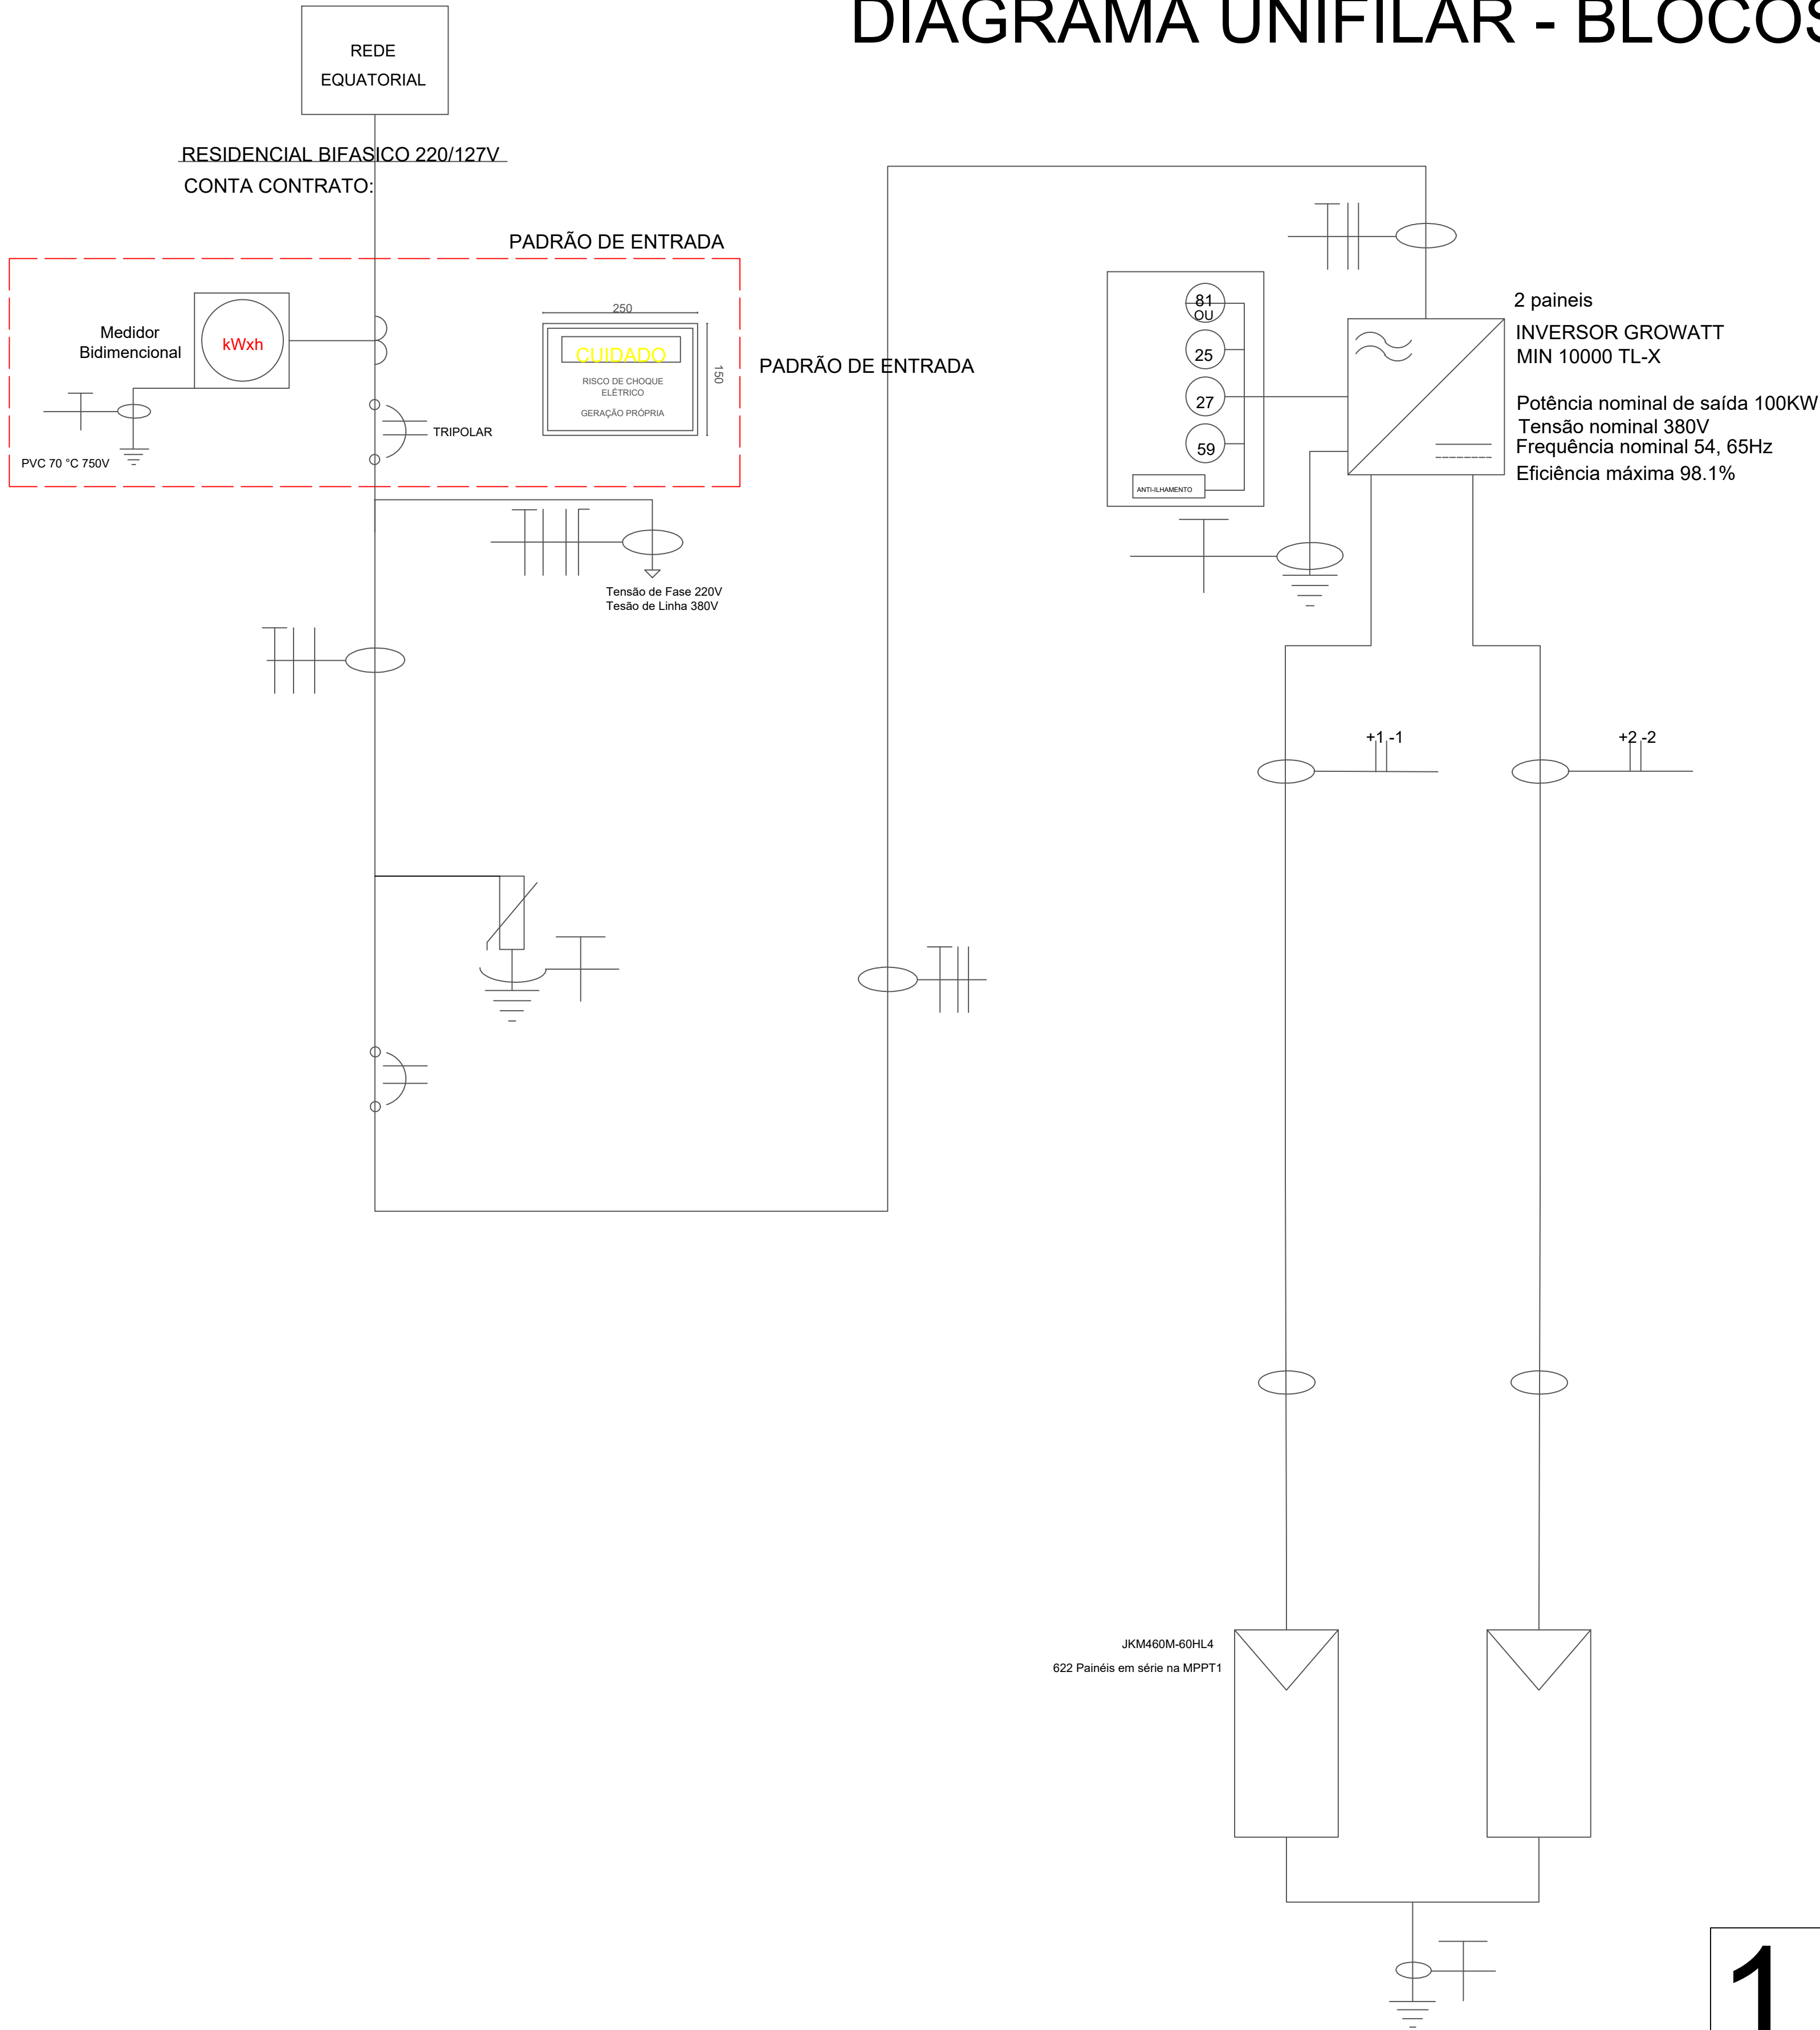

1/1

REQUERENTE	CONSUMIDOR PROPRIO	RESPONSÁVEL	ELETRIC SERVIÇOS ENG.	CREA	89313135272
LOCAL	RESIDENCIAL	DESENHO	RUAN LASTRINE	DATA	
DESCRIÇÃO	PROJETO ELETRICO DIMENSIONAMENTO DE UFT ON GRID	ESCALA	SEM ESCALA		
CONTEÚDO	PROJETO ELETRICO DE UFT				

Elétric Serviços Engenharia
CNPJ 18.165.794/0001-17